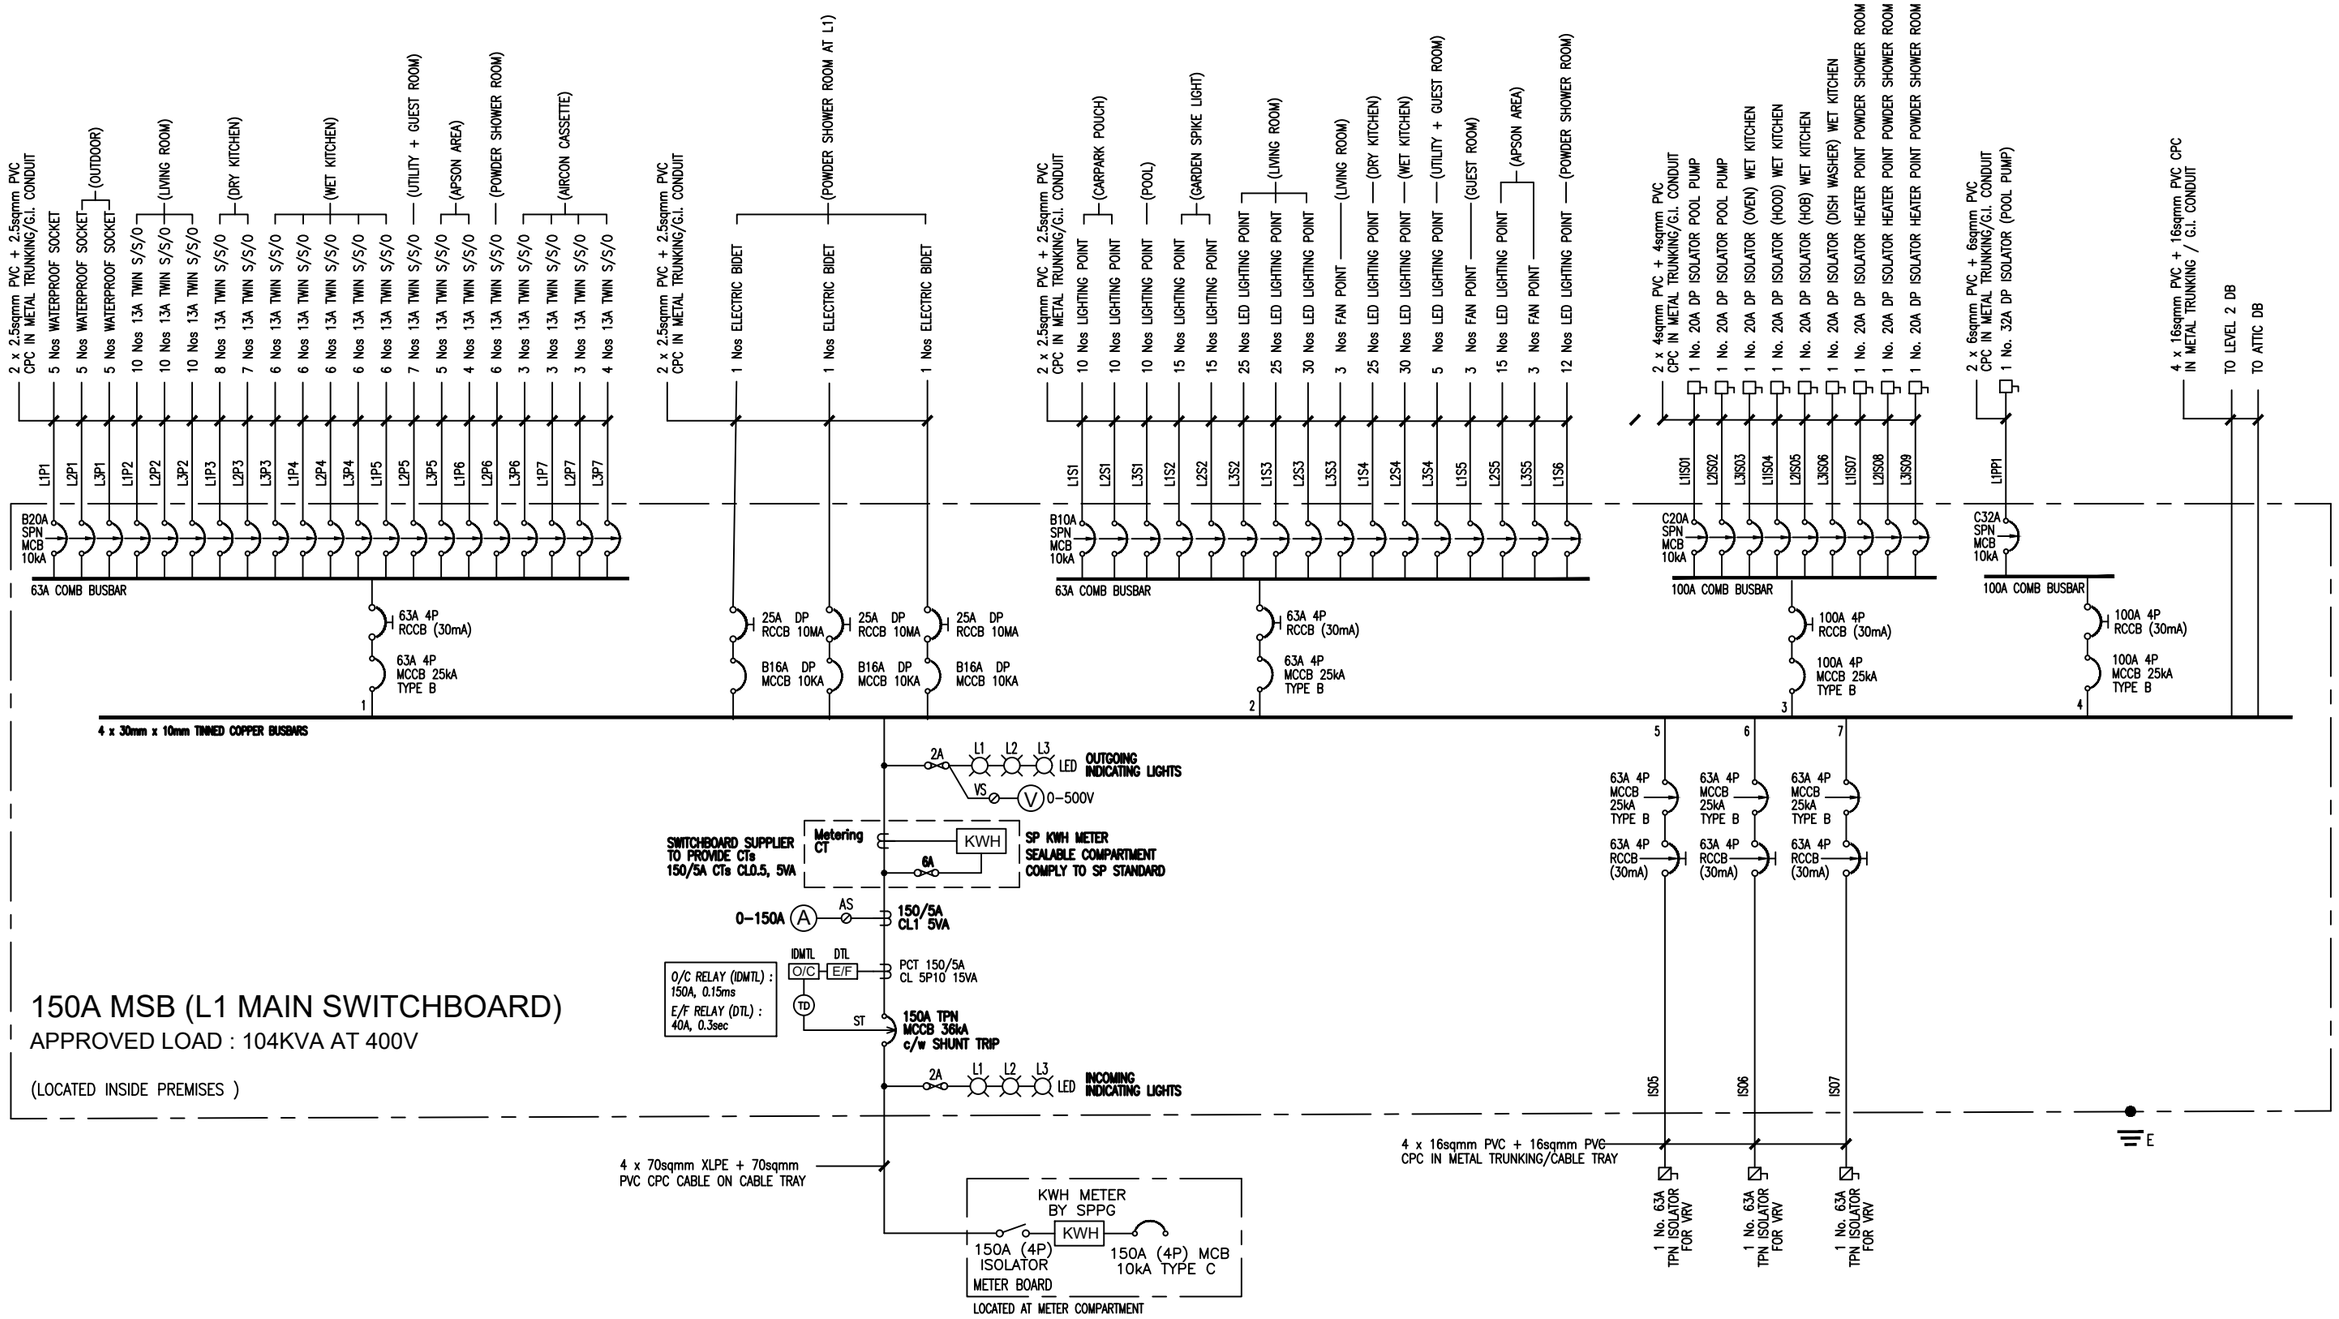

PROJECT CLIENT/OWNER ADDRESS :	ELECTRICAL CONTRACTOR :	JOB TITLE :	DRAWING TITLE :	CHECKED : Ryan	SCALE : N. T. S.
PROPOSED ERECTION OF A PAIR OF 2-STOREY ENVELOPE CONTROL SEMI-DETACHED DWELLING HOUSE WITH ATTIC AND A 2-STOREY ENVELOPE CONTROL DETACHED DWELLING HOUSE WITH ATTIC ON LOT 00594L MK02 AT 96 FARRER ROAD SINGAPORE 259225 (TANGLIN PLANNING AREA	i2R M&E PTE. LTD. Block 709 Yishun Avenue 5 #01-K1 Singapore 760709	PROPOSED ELECTRICAL SERVICES AT 96 FARRER ROAD SINGAPORE 259225	96+A+B 1ST FLOOR TOTAL ELECTRICAL INSTALLATION 150A MAIN SWITCH BOARD SINGLE LINE DIAGRAM	DRAWN : NCS	DATE : 30 NOV 2024
				DRAWING NO. : i2R-96FR-E-SL1	REV : 0

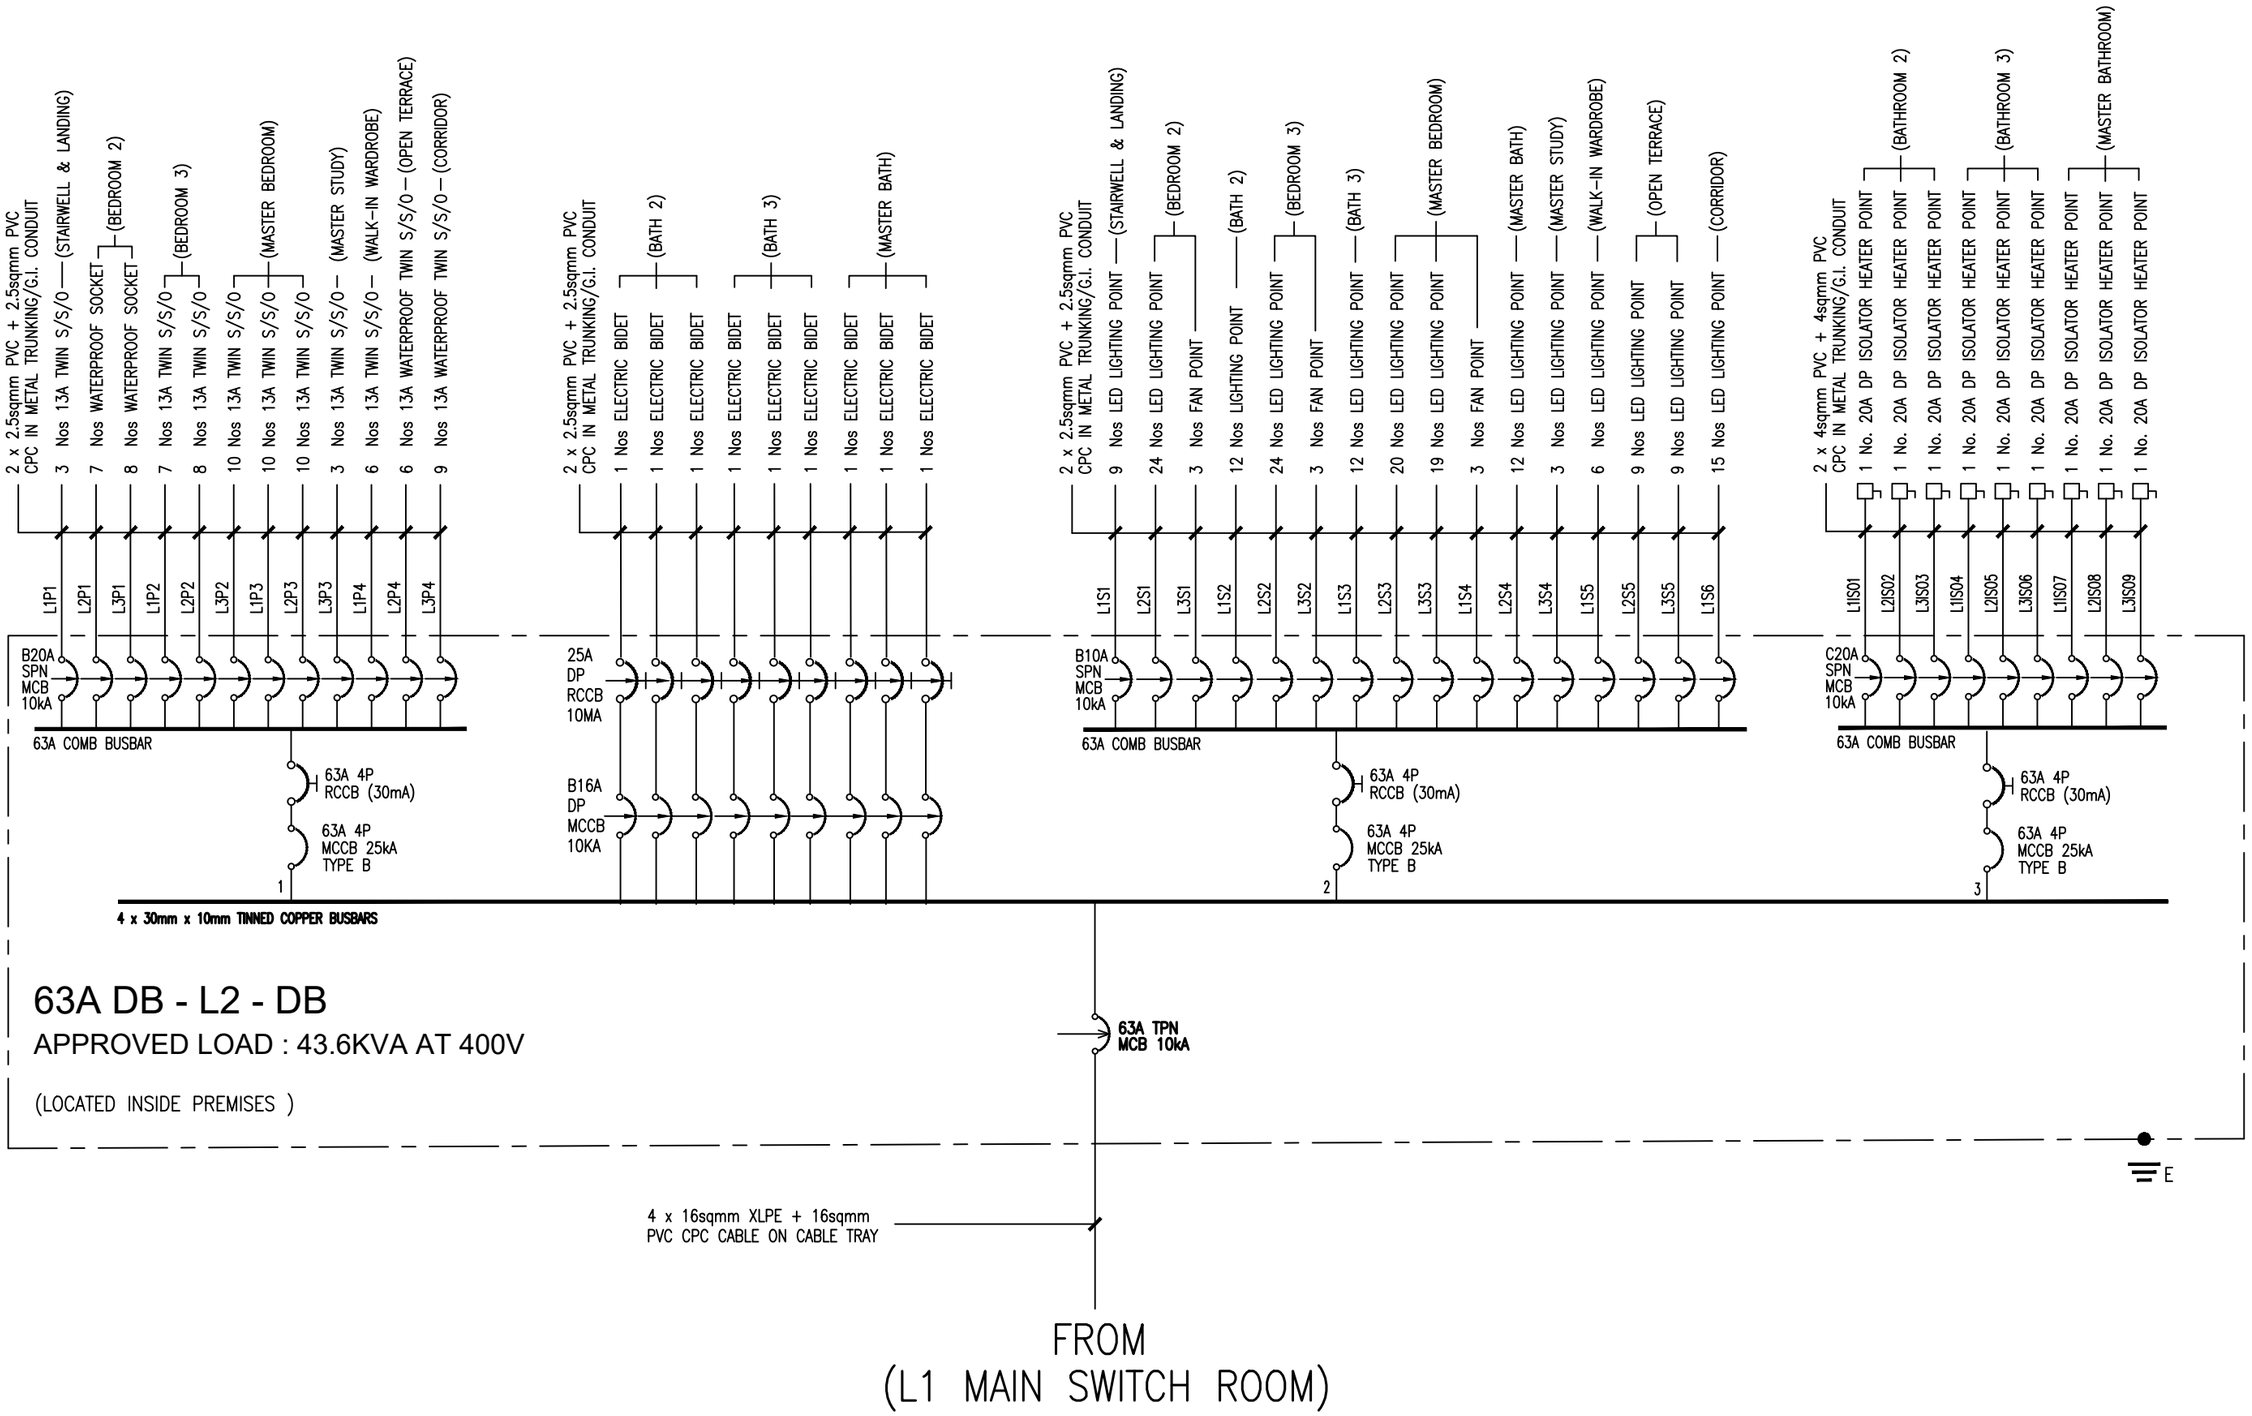

PROJECT CLIENT/OWNER ADDRESS :	ELECTRICAL CONTRACTOR :	JOB TITLE :	DRAWING TITLE :	CHECKED : Ryan	SCALE : N. T. S.
PROPOSED ERECTION OF A PAIR OF 2-STOREY ENVELOPE CONTROL SEMI-DETACHED DWELLING HOUSE WITH ATTIC AND A 2-STOREY ENVELOPE CONTROL DETACHED DWELLING HOUSE WITH ATTIC ON LOT 00594L MK02 AT 96 FARRER ROAD SINGAPORE 259225 (TANGLIN PLANNING AREA	i2R M&E PTE. LTD. Block 709 Yishun Avenue 5 #01-K1 Singapore 760709	PROPOSED ELECTRICAL SERVICES AT 96 FARRER ROAD SINGAPORE 259225	96+A+B 2ND FLOOR TOTAL ELECTRICAL INSTALLATION 150A MAIN SWITCH BOARD SINGLE LINE DIAGRAM	DRAWN : NCS	DATE : 30 NOV 2024
				DRAWING NO. : i2R-96FR-E-SL1	REV : 0

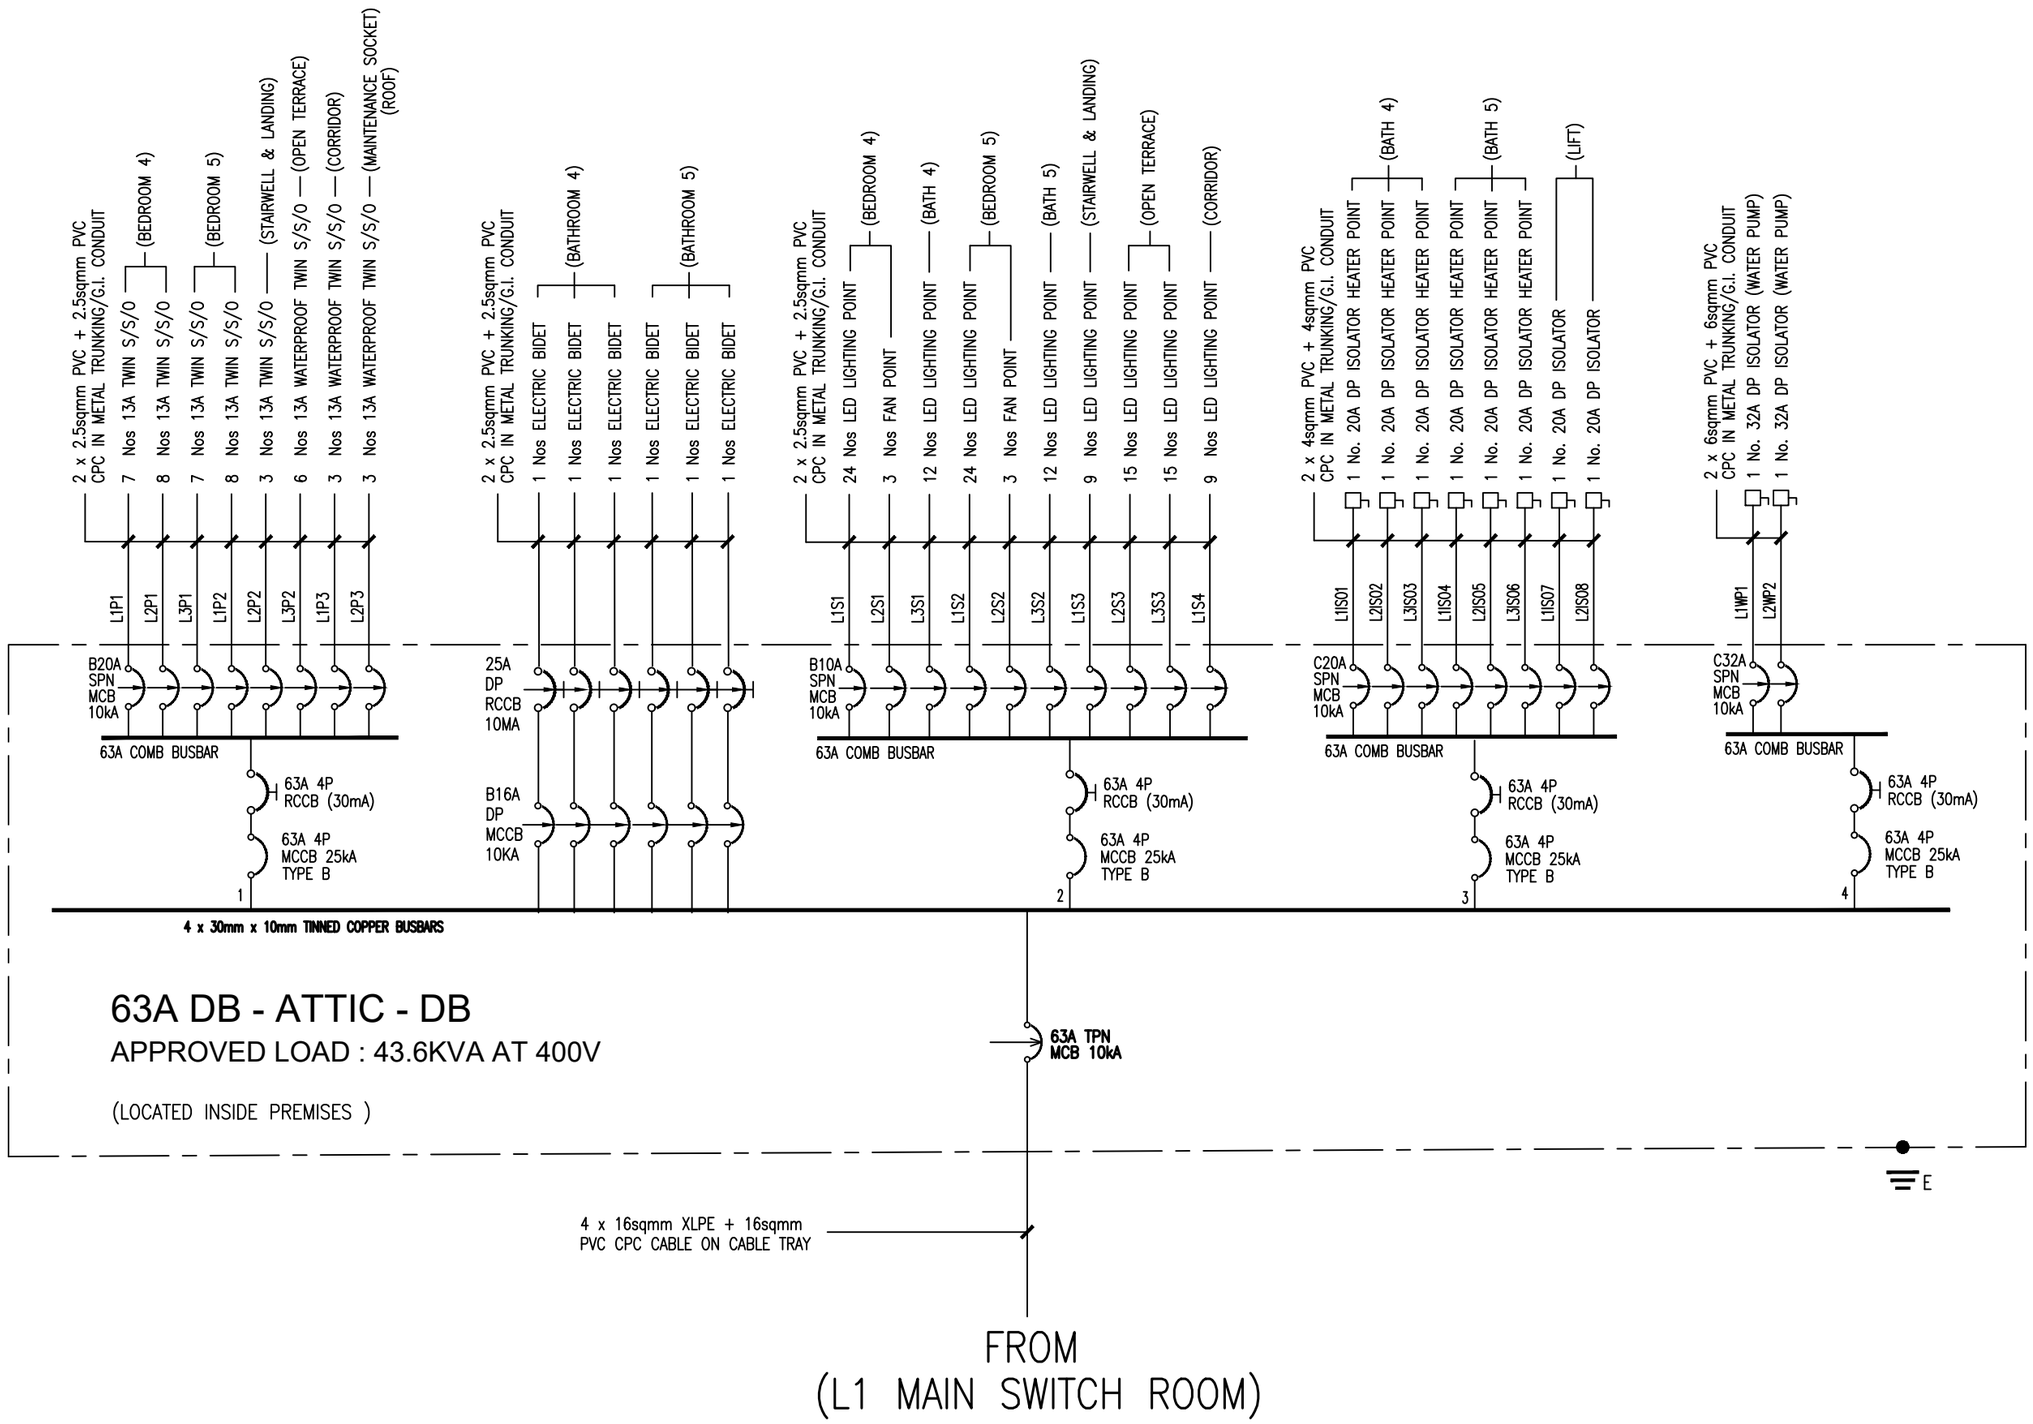

PROJECT CLIENT/OWNER ADDRESS :	ELECTRICAL CONTRACTOR :	JOB TITLE :	DRAWING TITLE :	CHECKED : Ryan	SCALE : N. T. S.
PROPOSED ERECTION OF A PAIR OF 2-STOREY ENVELOPE CONTROL SEMI-DETACHED DWELLING HOUSE WITH ATTIC AND A 2-STOREY ENVELOPE CONTROL DETACHED DWELLING HOUSE WITH ATTIC ON LOT 00594L MK02 AT 96 FARRER ROAD SINGAPORE 259225 (TANGLIN PLANNING AREA	i2R M&E PTE. LTD. Block 709 Yishun Avenue 5 #01-K1 Singapore 760709	PROPOSED ELECTRICAL SERVICES AT 96 FARRER ROAD SINGAPORE 259225	96+A+B ATTIC TOTAL ELECTRICAL INSTALLATION 150A MAIN SWITCH BOARD SINGLE LINE DIAGRAM	DRAWN : NCS	DATE : 30 NOV 2024
				DRAWING NO. : i2R-96FR-E-SL1	REV : 0