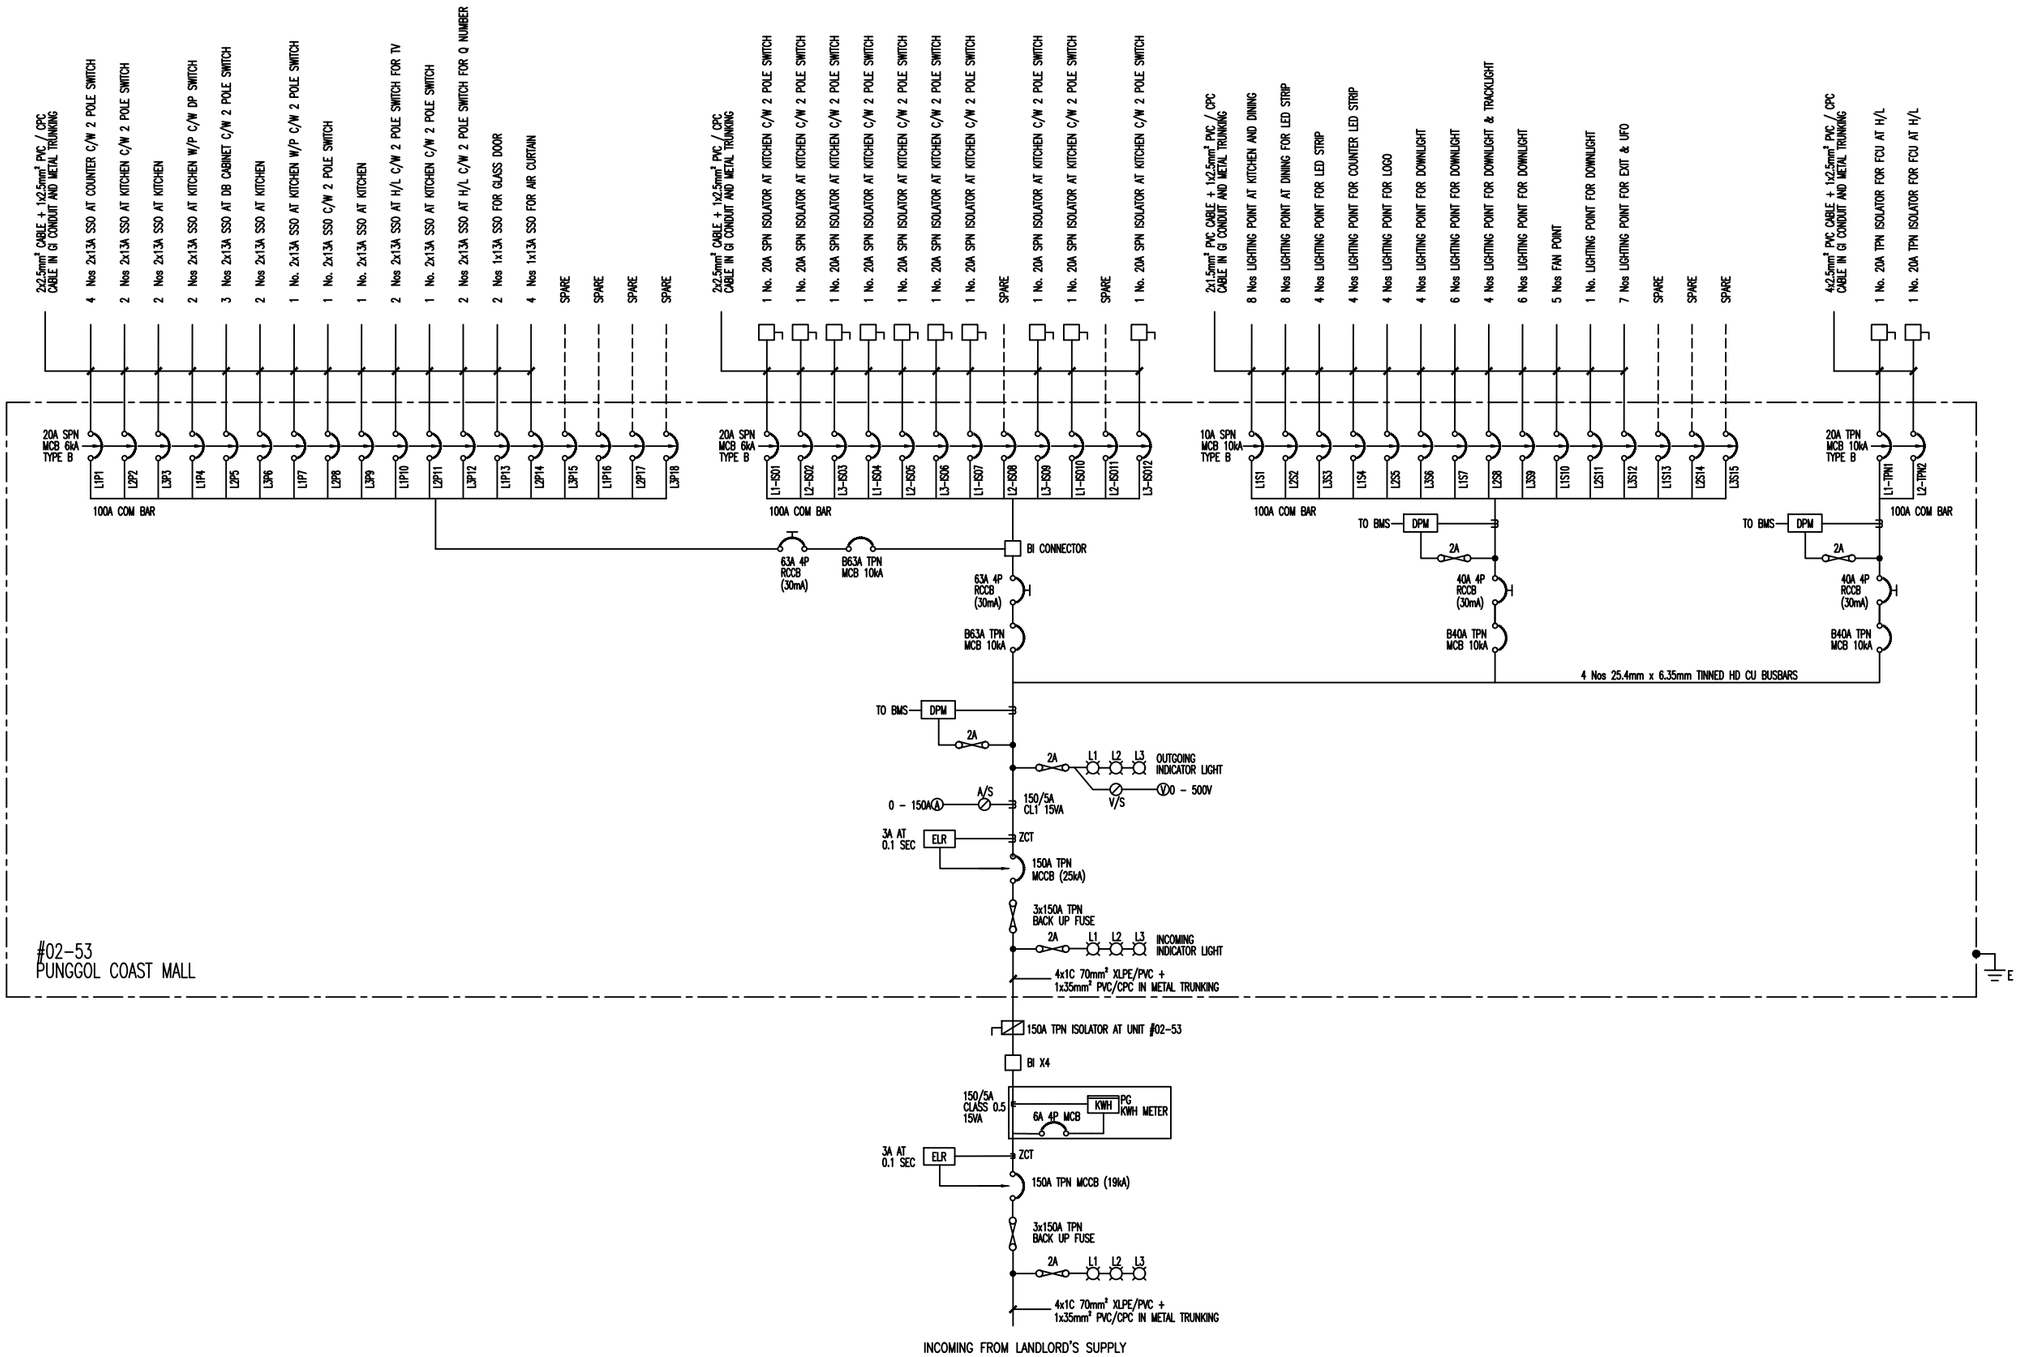

CLIENT / ADDRESS :	MAIN CONTRACTOR :	ELECTRICAL CONTRACTOR :	DRAWING TITLE :	LEW :	CHECKED :	DATE :
TASTYJOY PTE LTD YA KUN KAYA TOAST @ PUNGGOL COAST MALL #02-53, 84 PUNGGOL WAY, SINGAPORE 829911			SINGLE LINE DIAGRAM (SLD)	ABDUL JABBAR EMA Licence No. : 8/35550	Ryan	26 JAN 2026
					DRAWING NO. : I2R-YKKT-PCM-SLD	REV : 0