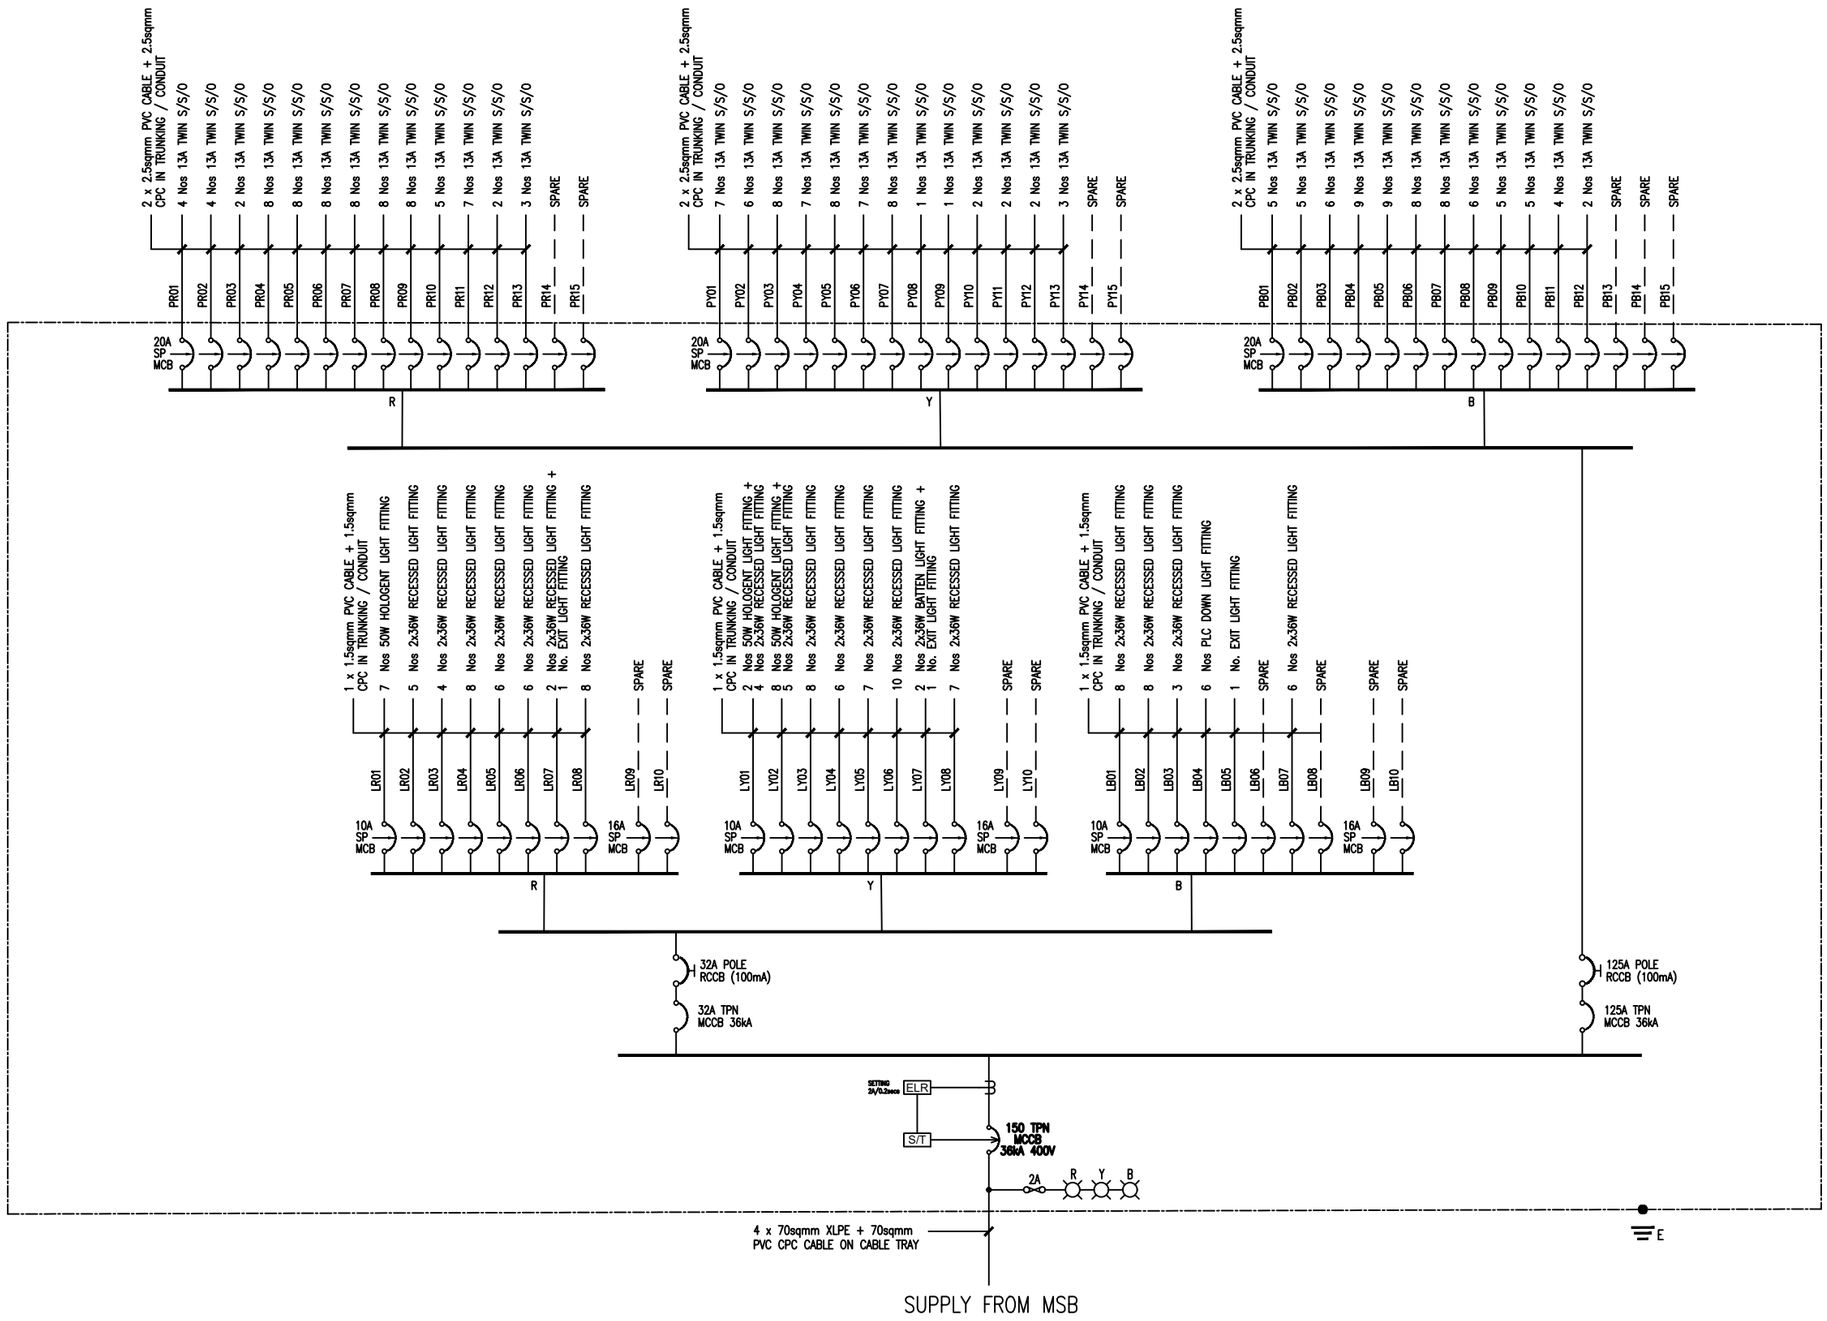

CLIENT / ADDRESS :	MAIN CONTRACTOR :	ELECTRICAL CONTRACTOR :	DRAWING TITLE :	LEW :	CHECKED :	DATE :
Luqiang Electromecahnical Engineering (Singapore) Pte Ltd 19 Senoko Loop #04-00 Singapore 758168		I2R M&E PTE. LTD. 709 Yishun Avenue 5 #01-K1 Singapore 760709 TEL: 9777 1983	SINGLE LINE DIAGRAM (SLD)		Ryan	14 APR 2025
					DRAWING NO. : I2R-LEE-SNK-SLD	REV : 0