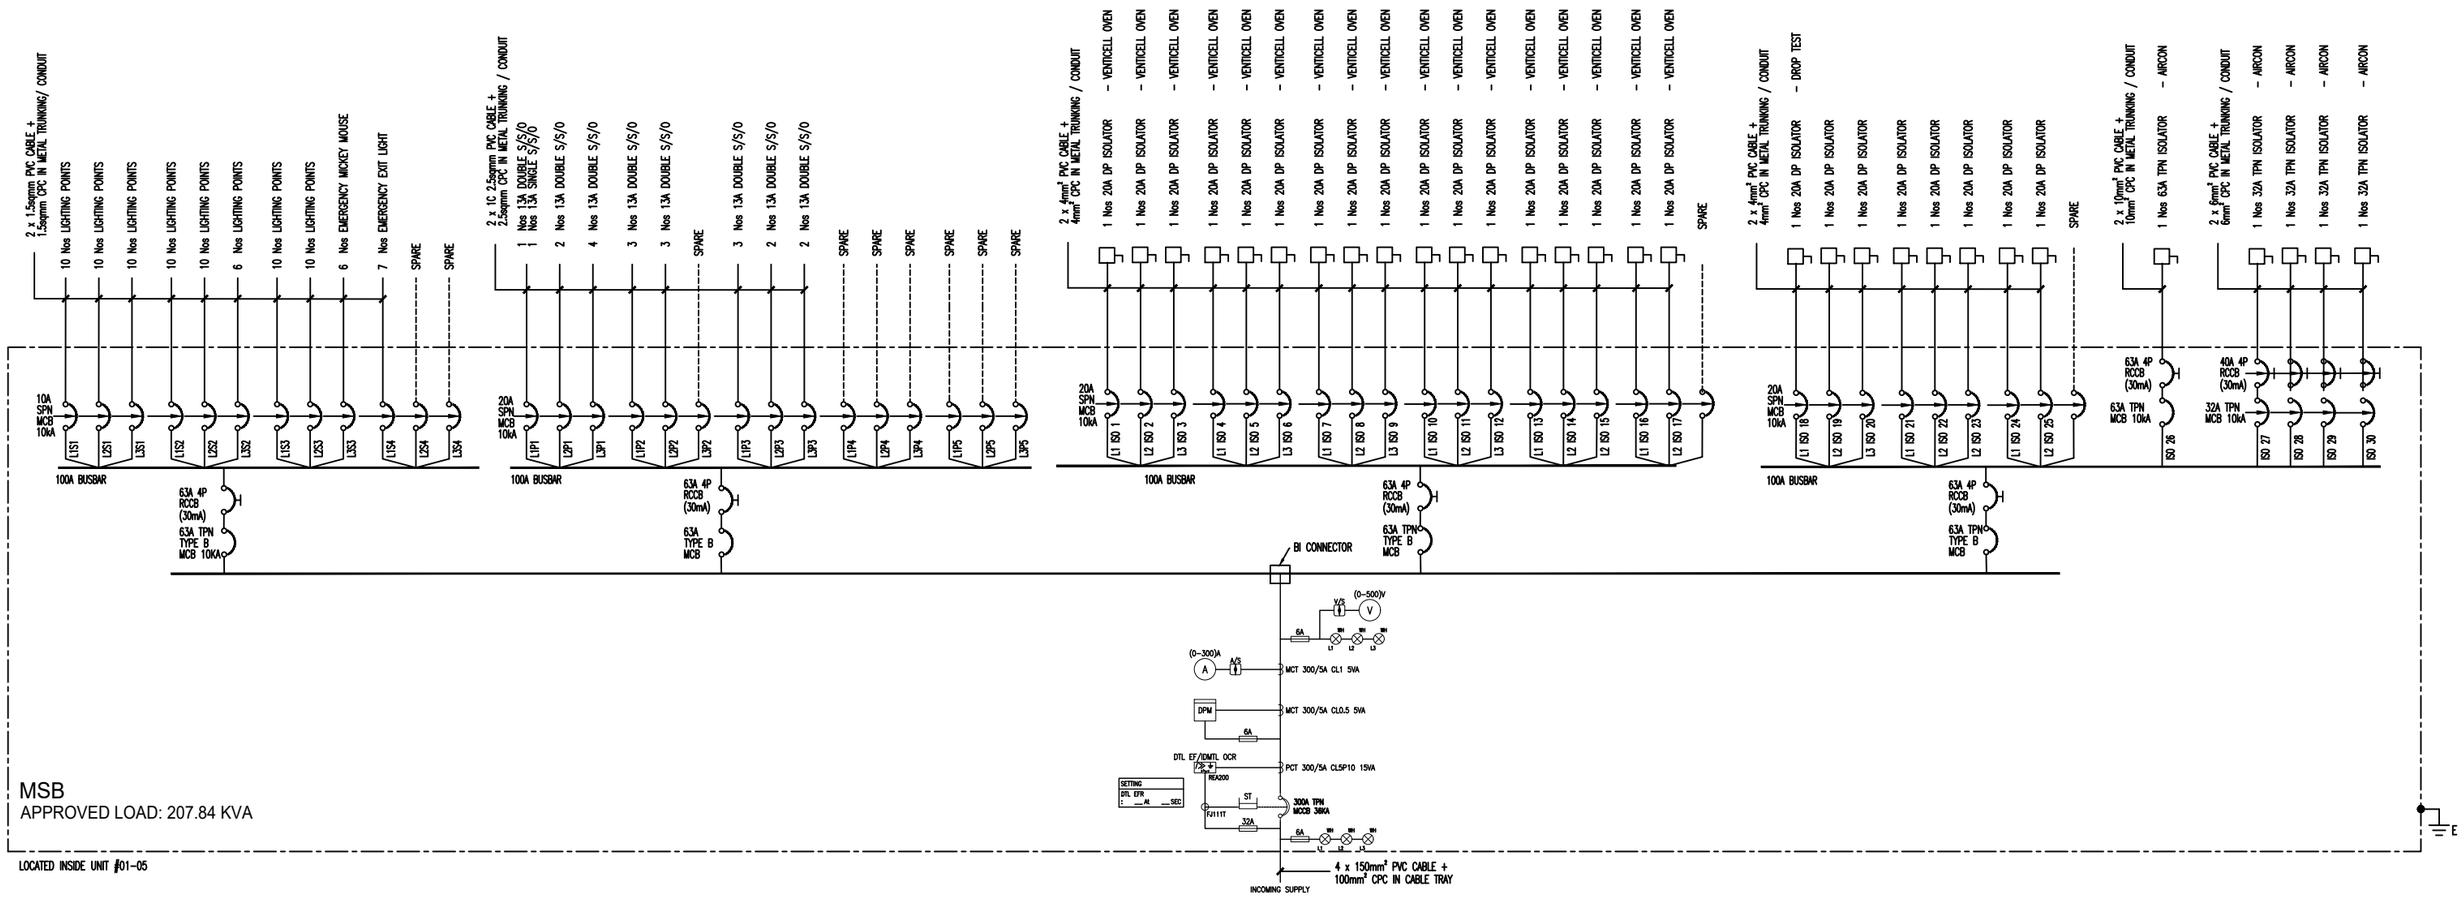

CLIENT / ADDRESS :	MAIN CONTRACTOR :	ELECTRICAL CONTRACTOR :	PROJECT TITLE :	LEW :	CHECKED :	DATE :
TRIO TECH INTERNATIONAL PTE LTD 1004 TOA PAYOH NORTH #01-03/05 S 318995	HUNT WAY MANAGEMENT CONSULTANCY SERVICES 21 Bukit Batok Crescent, WCEGA Tower, #11-71 Singapore 658065	I2R M&E PTE. LTD. 709 Yishun Avenue 5 #01-K1 Singapore 760709 TEL: 9777 1983	Electrical Single Line Drawing at Block 1004 #01-03/05 Toa Payoh North S 318996	SEOW SWEE LEONG EMA Licence No. : 8/25825	Ryan	1 OCT 2025
					DRAWING NO. : I2R-TTI-TPYN-SLD	REV : 0