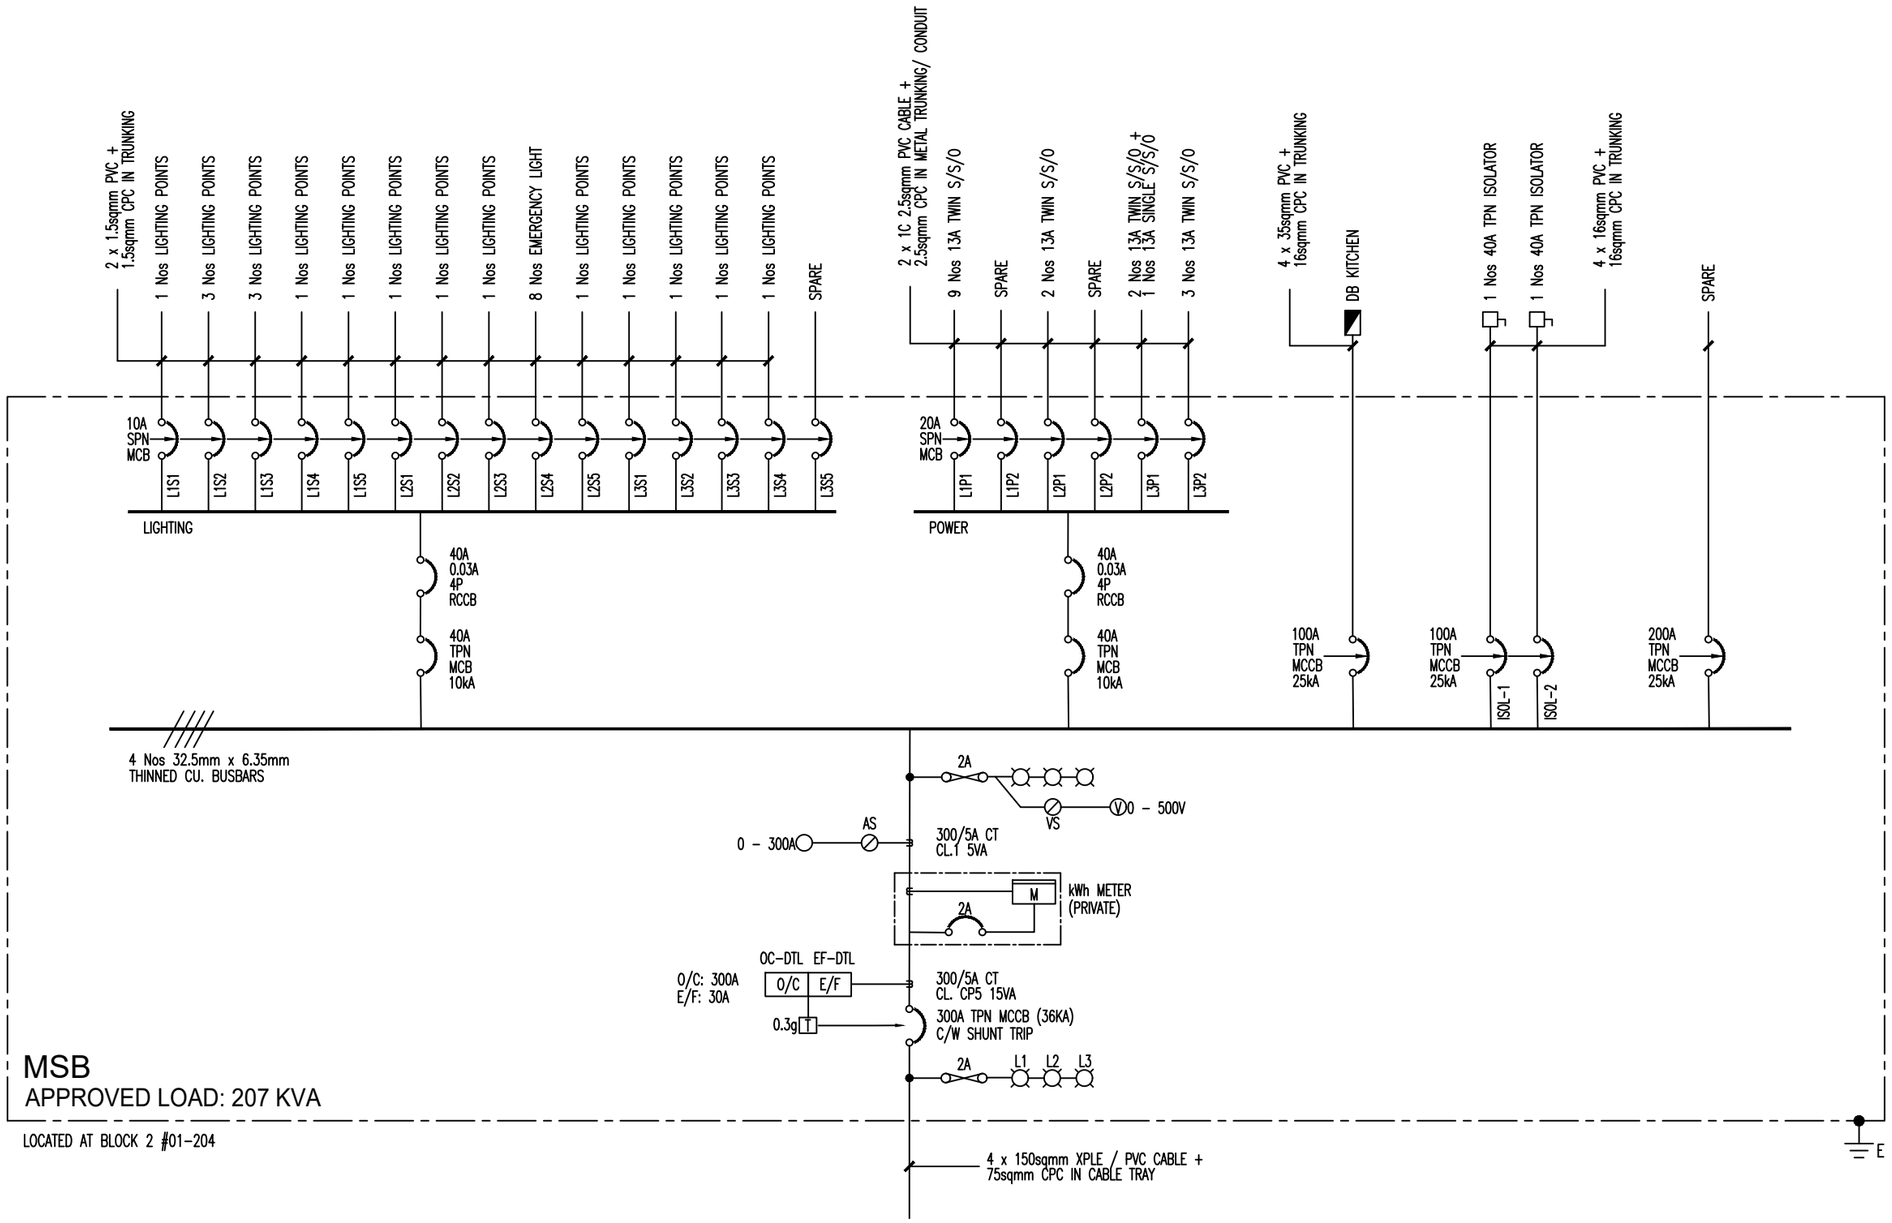

CLIENT / ADDRESS :	MAIN CONTRACTOR :	ELECTRICAL CONTRACTOR :	DRAWING TITLE :	LEW :	CHECKED :	DATE :
CAYENNE'S CAFE LLP 8 Somapah Road #01-204 Building 2, SUTD Singapore 487372	I2R M&E PTE. LTD. 709 Yishun Avenue 5 #01-K1 Singapore 760709 TEL: 9777 1983	I2R M&E PTE. LTD. 709 Yishun Avenue 5 #01-K1 Singapore 760709 TEL: 9777 1983	SINGLE LINE DIAGRAM (SLD)	SEOW SWEE LEONG EMA License No : 8/25825	Ryan	13 APR 2025
					DRAWING NO. : I2R-CCL-SUTD-SLD	REV : 0