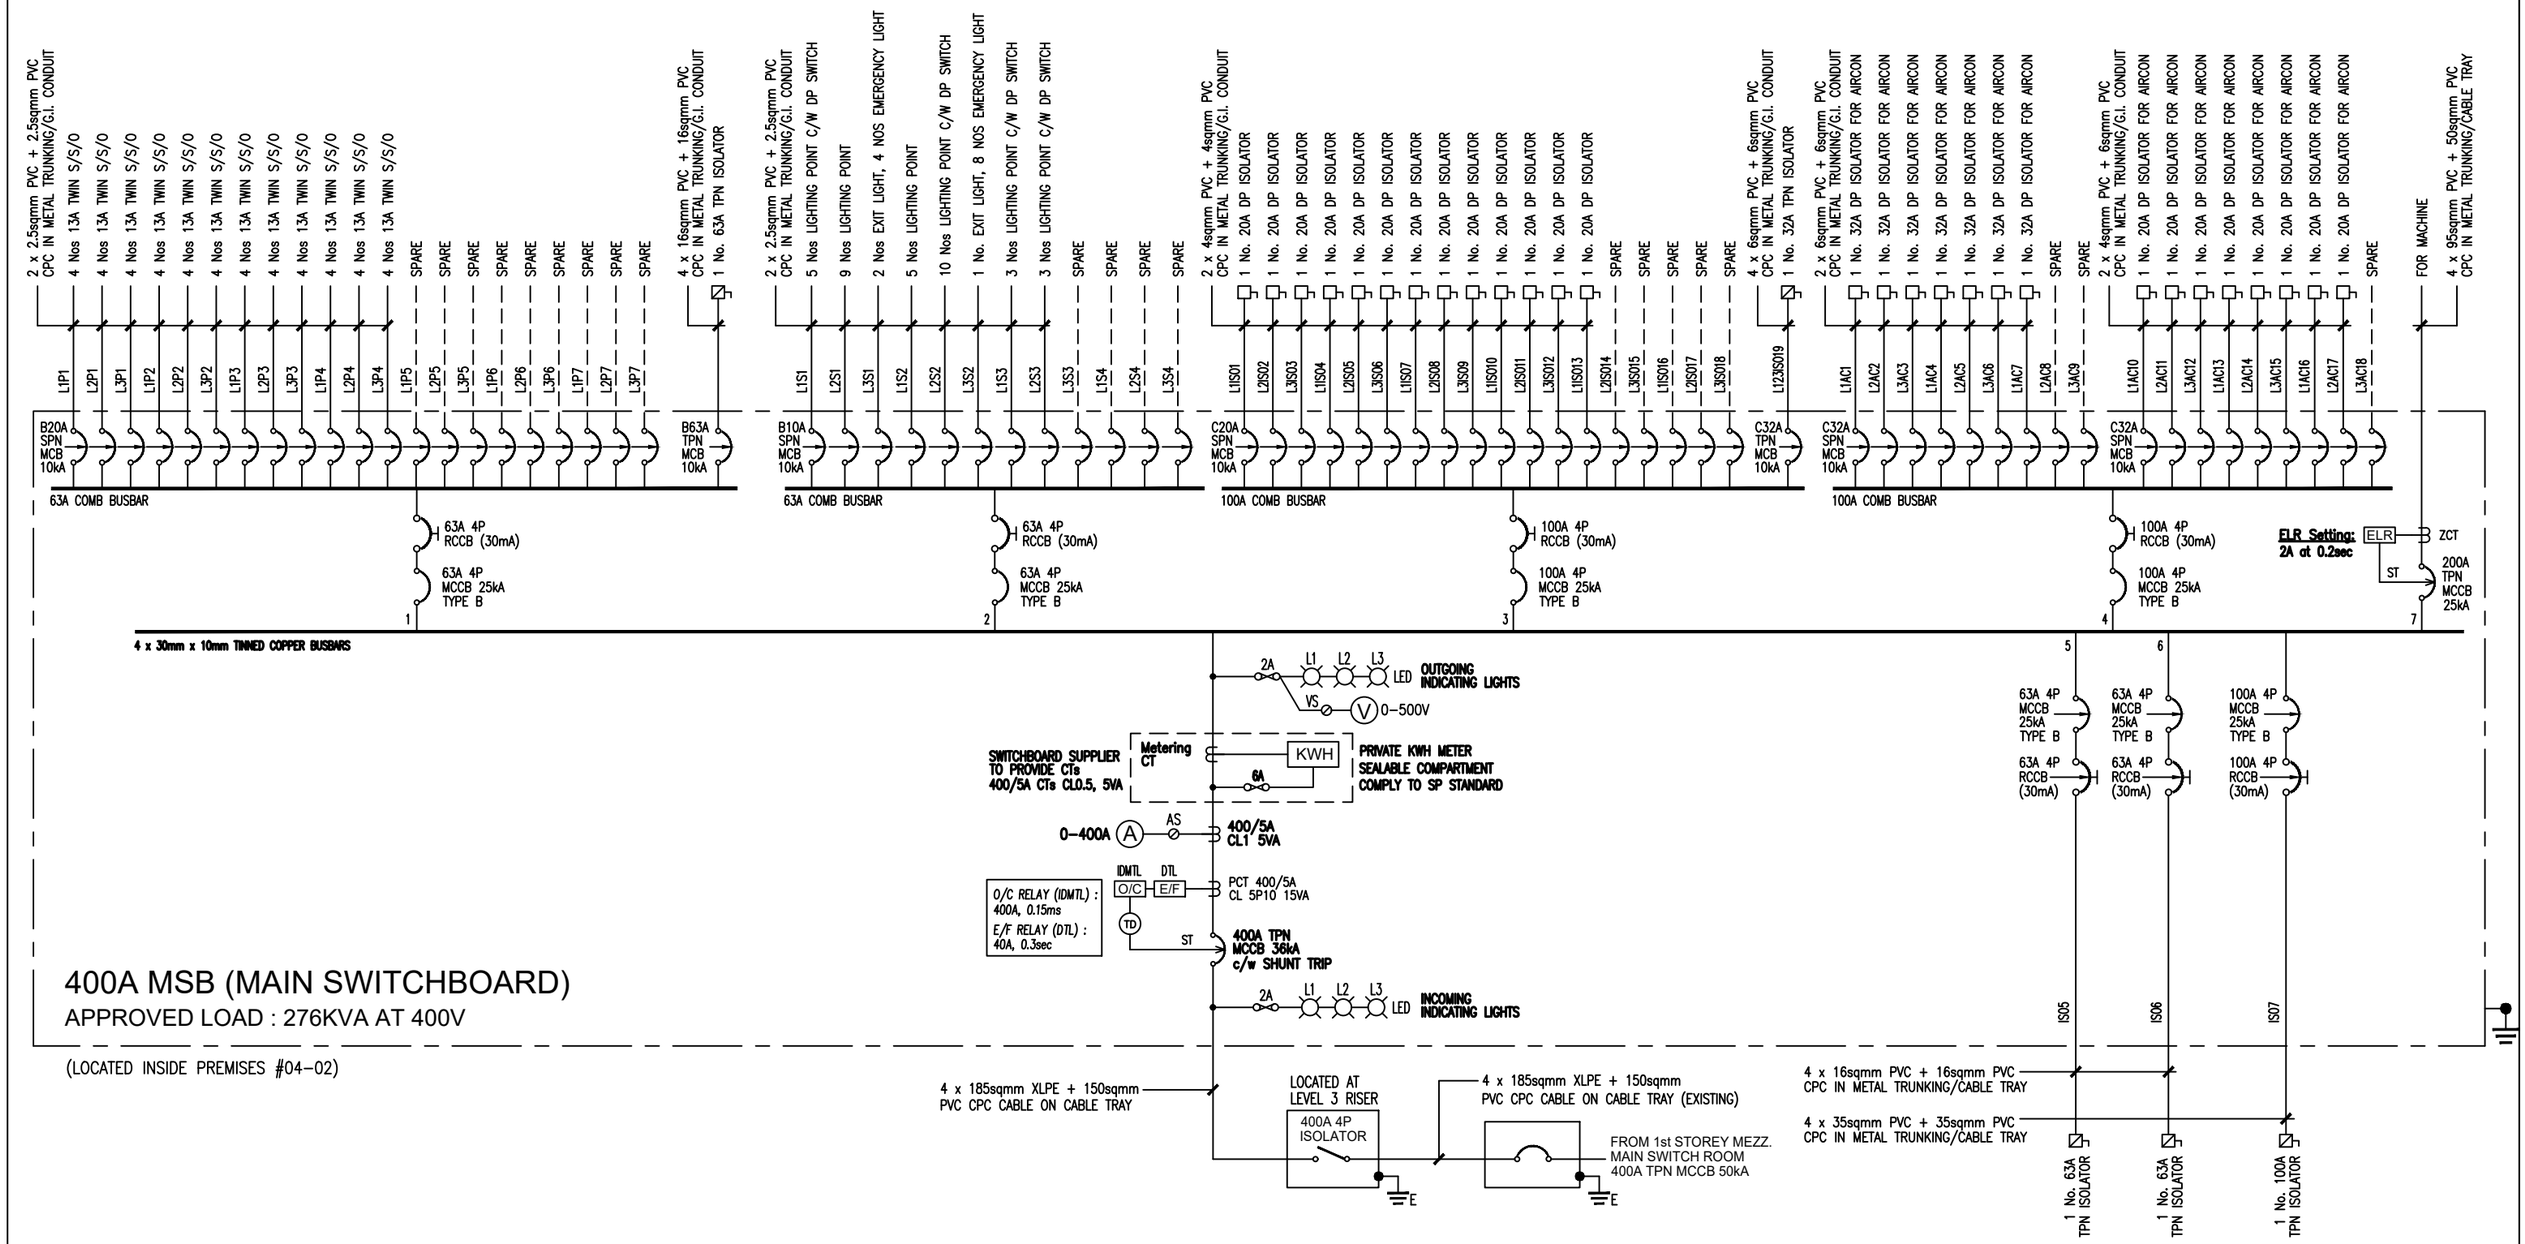

PROJECT CLIENT/OWNER ADDRESS :	ELECTRICAL CONTRACTOR :	JOB TITLE :	DRAWING TITLE :	CHECKED : Ryan	SCALE : N. T. S.
ALIENA PTE LTD No. 6 UBI VIEW #04-02 SINGAPORE 408544	i2R M&E PTE. LTD. Block 709 Yishun Avenue 5 #01-K1 Singapore 760709	PROPOSED ELECTRICAL SERVICES AT THE #04-02 No. 6 UBI VIEW SINGAPORE 408544	ELECTRICAL INSTALLATION 400A MAIN SWITCH BOARD SINGLE LINE DIAGRAM	DRAWN : DC	DATE : 23 Oct 2024
				DRAWING NO. : i2R-ALN-E-SL1	REV : 0