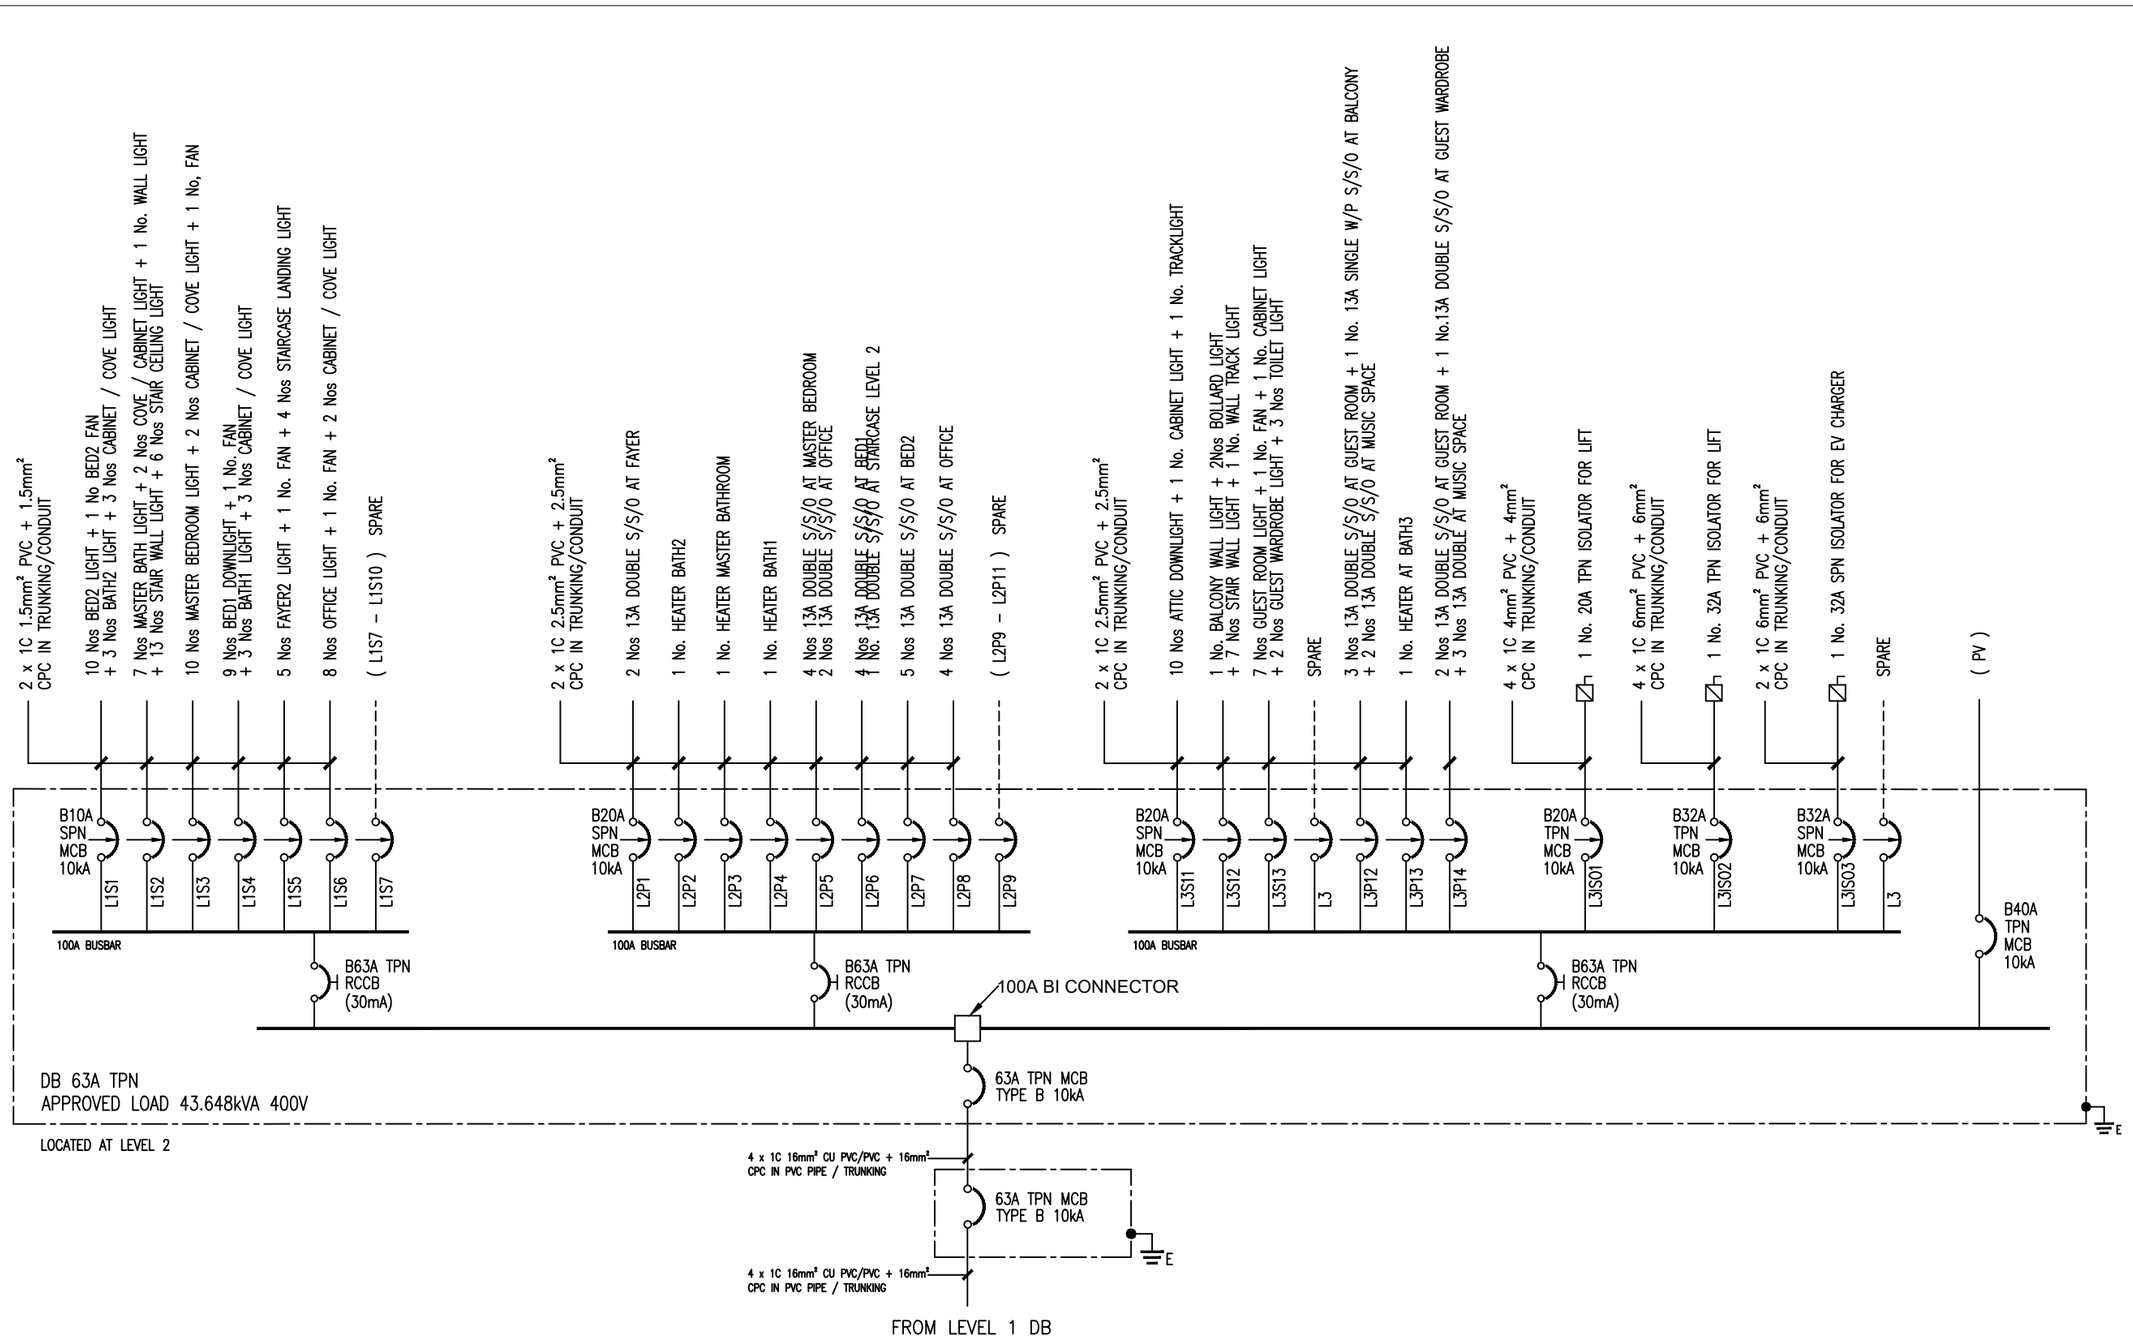

CLIENT / ADDRESS :	MAIN CON:	ELECTRIC CONTRACTOR:	DRAWING TITLE :		DRAWN BY:	DATE :
77 COWDRAY AVE SINGAPORE 558078	NEXUS II PTE LTD	UC ELECTRICAL PTE LTD	ELECTRICAL SERVICES SINGLE LINE DIAGRAM (SLD) LEVEL 2		NCS	15 FEB 2026
					DRAWING NO. : NEX-UC-CDA-SLD-LV2	REV : 0