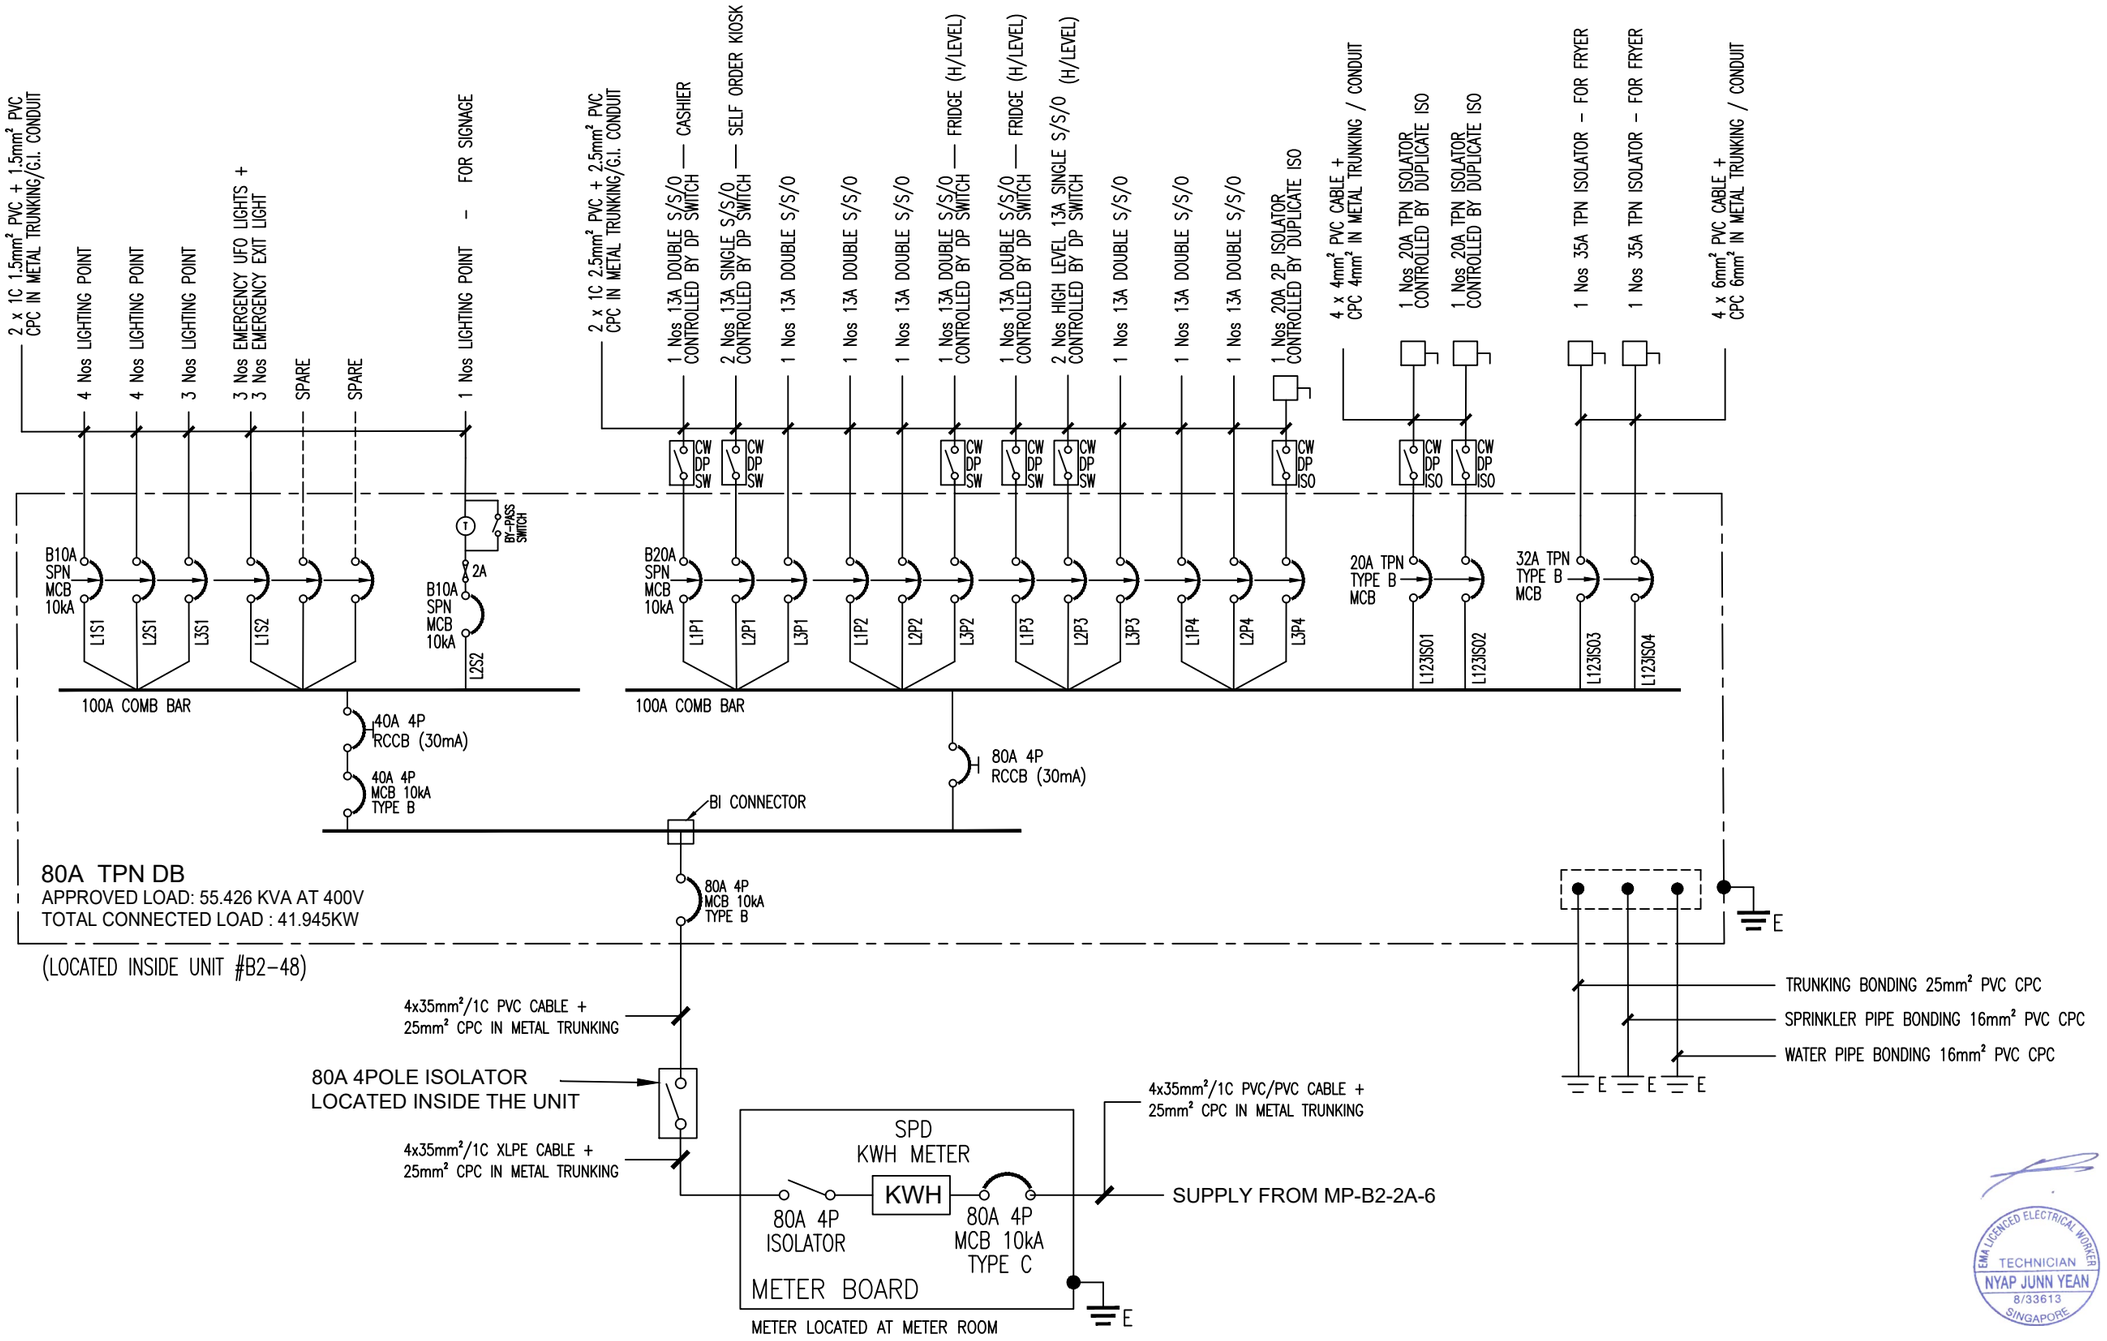

CLIENT / ADDRESS :	MAIN CONTRACTOR :	ELECTRICAL CONTRACTOR :	DRAWING TITLE :	LEW :	CHECKED :	DATE :
FIRST FRONTIER FOOD PTE LTD (GIRAFFA) Vivo City 1 HarbourFront Walk B2-48 S098585	3S FURNISHING AND ENGINEERING PTE LTD 1 NORTH BRIDGE ROAD #24-03 HIGH STREET CENTRE SINGAPORE 179094	I2R M&E PTE. LTD. 709 Yishun Avenue 5 #01-K1 Singapore 760709 TEL: 9777 1983	SINGLE LINE DIAGRAM (SLD)	Ryan, Nyap Junn Yean EMA Licence No. : 8/33613 Mobile Number. : 91597207	Ryan	16 JUL 2025
					DRAWING NO. : I2R-GRF-VVC-SLD	REV : 0