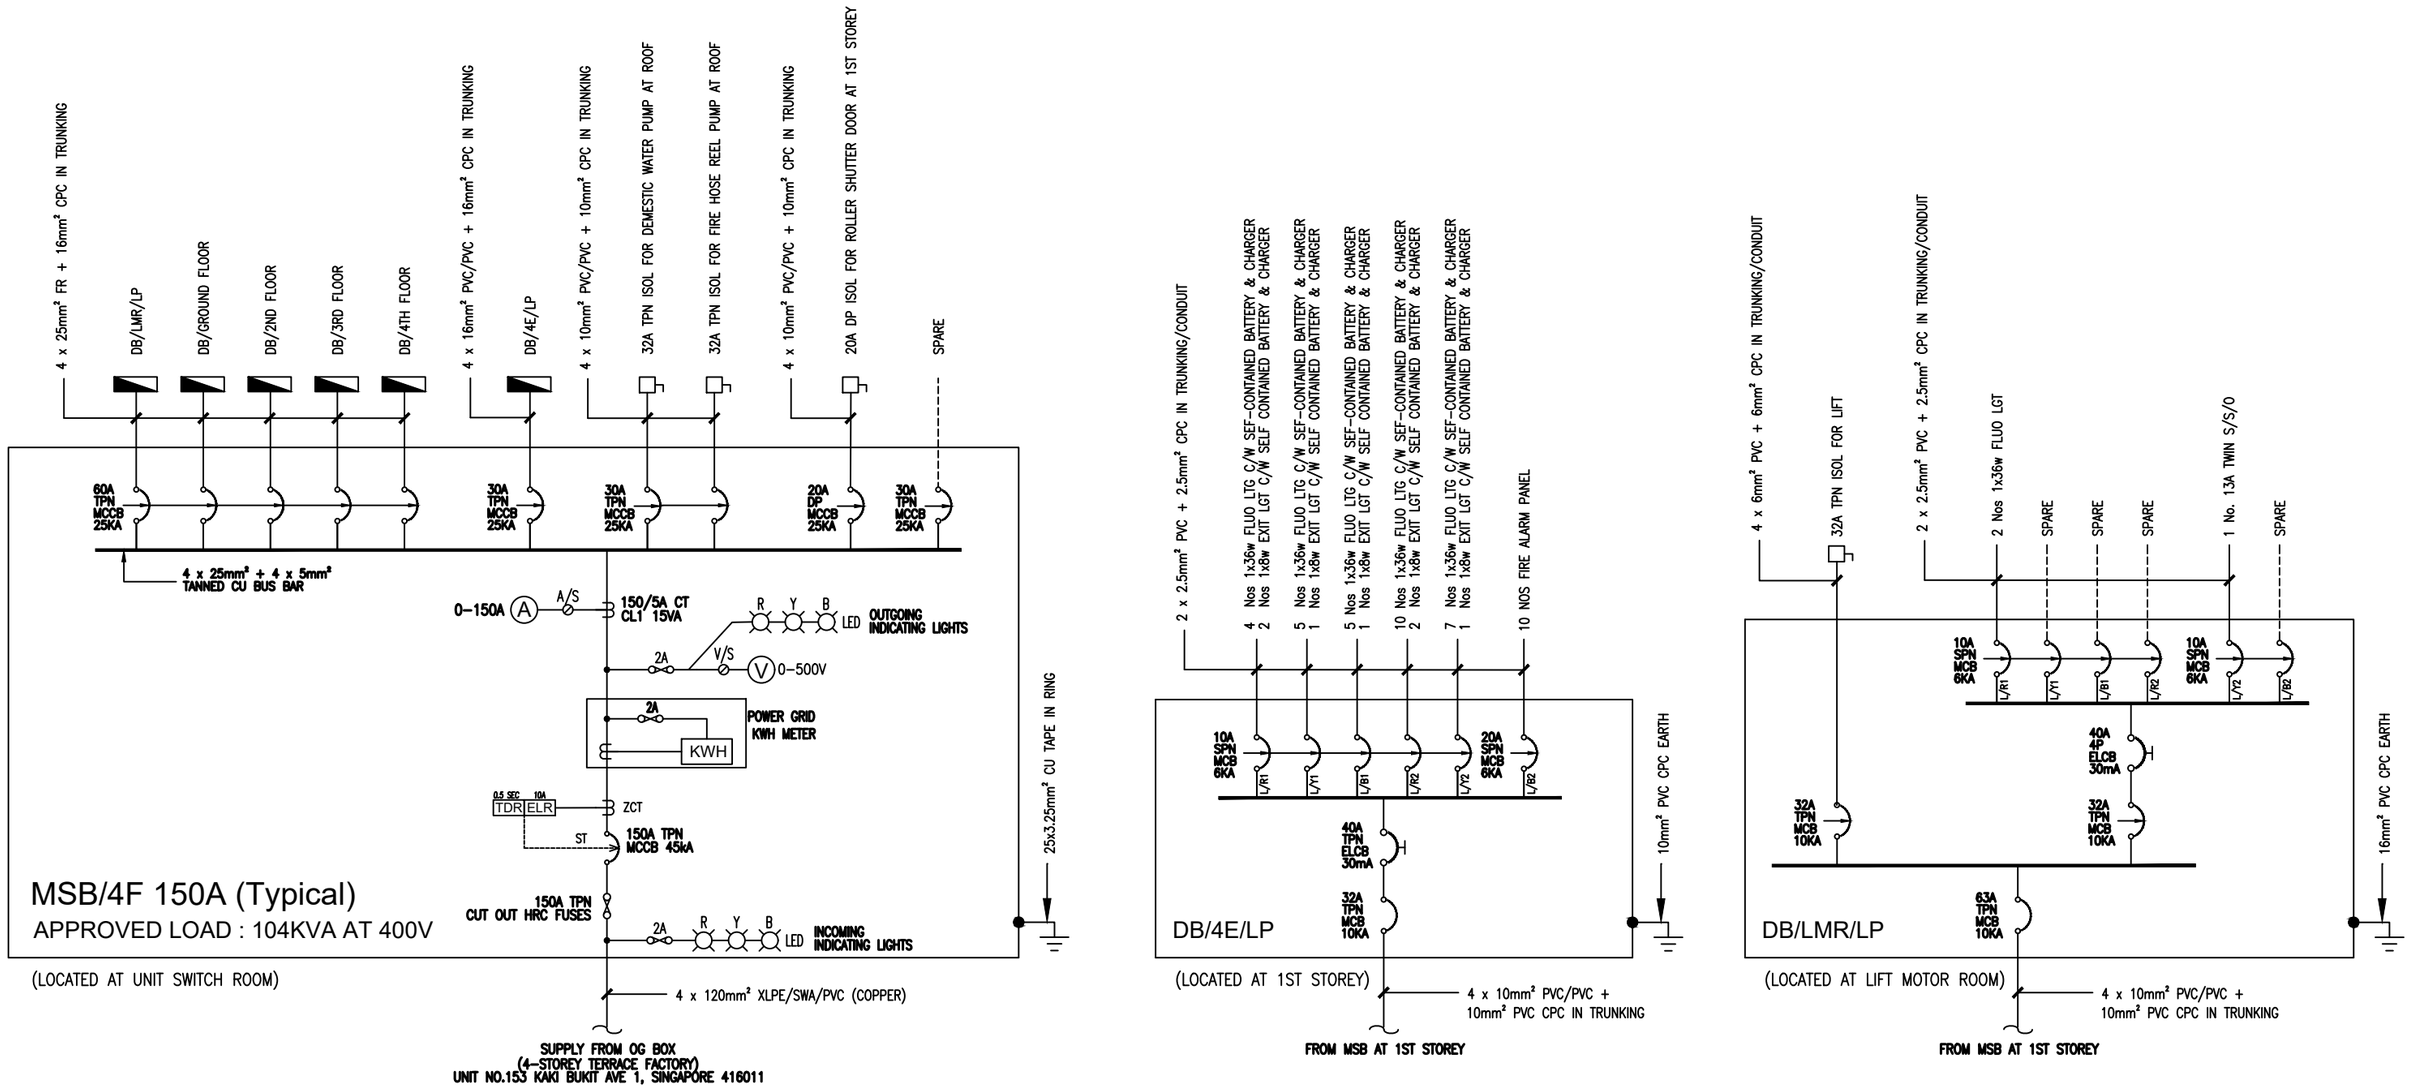

CLIENT / ADDRESS :	MAIN CONTRACTOR :	ELECTRICAL CONTRACTOR :	DRAWING TITLE :	LEW :	CHECKED :	DATE :
Mc Design & Solution Pte Ltd 153 KAKI BUKIT AVENUE 1 SINGAPORE 416011	Desmond Chan 421 Tagore Industrial Avenue #03-16 Tagore 8 S 787805	I2R M&E PTE. LTD. 709 Yishun Avenue 5 #01-K1 Singapore 760709 TEL: 9777 1983	SINGLE LINE DIAGRAM (SLD)	NYAP JUNN YEAN EMA Licence No. : 8/33613	Ryan	30/9/2025
					DRAWING NO. : I2R-MCDS-KBA1-SLD	REV : 0