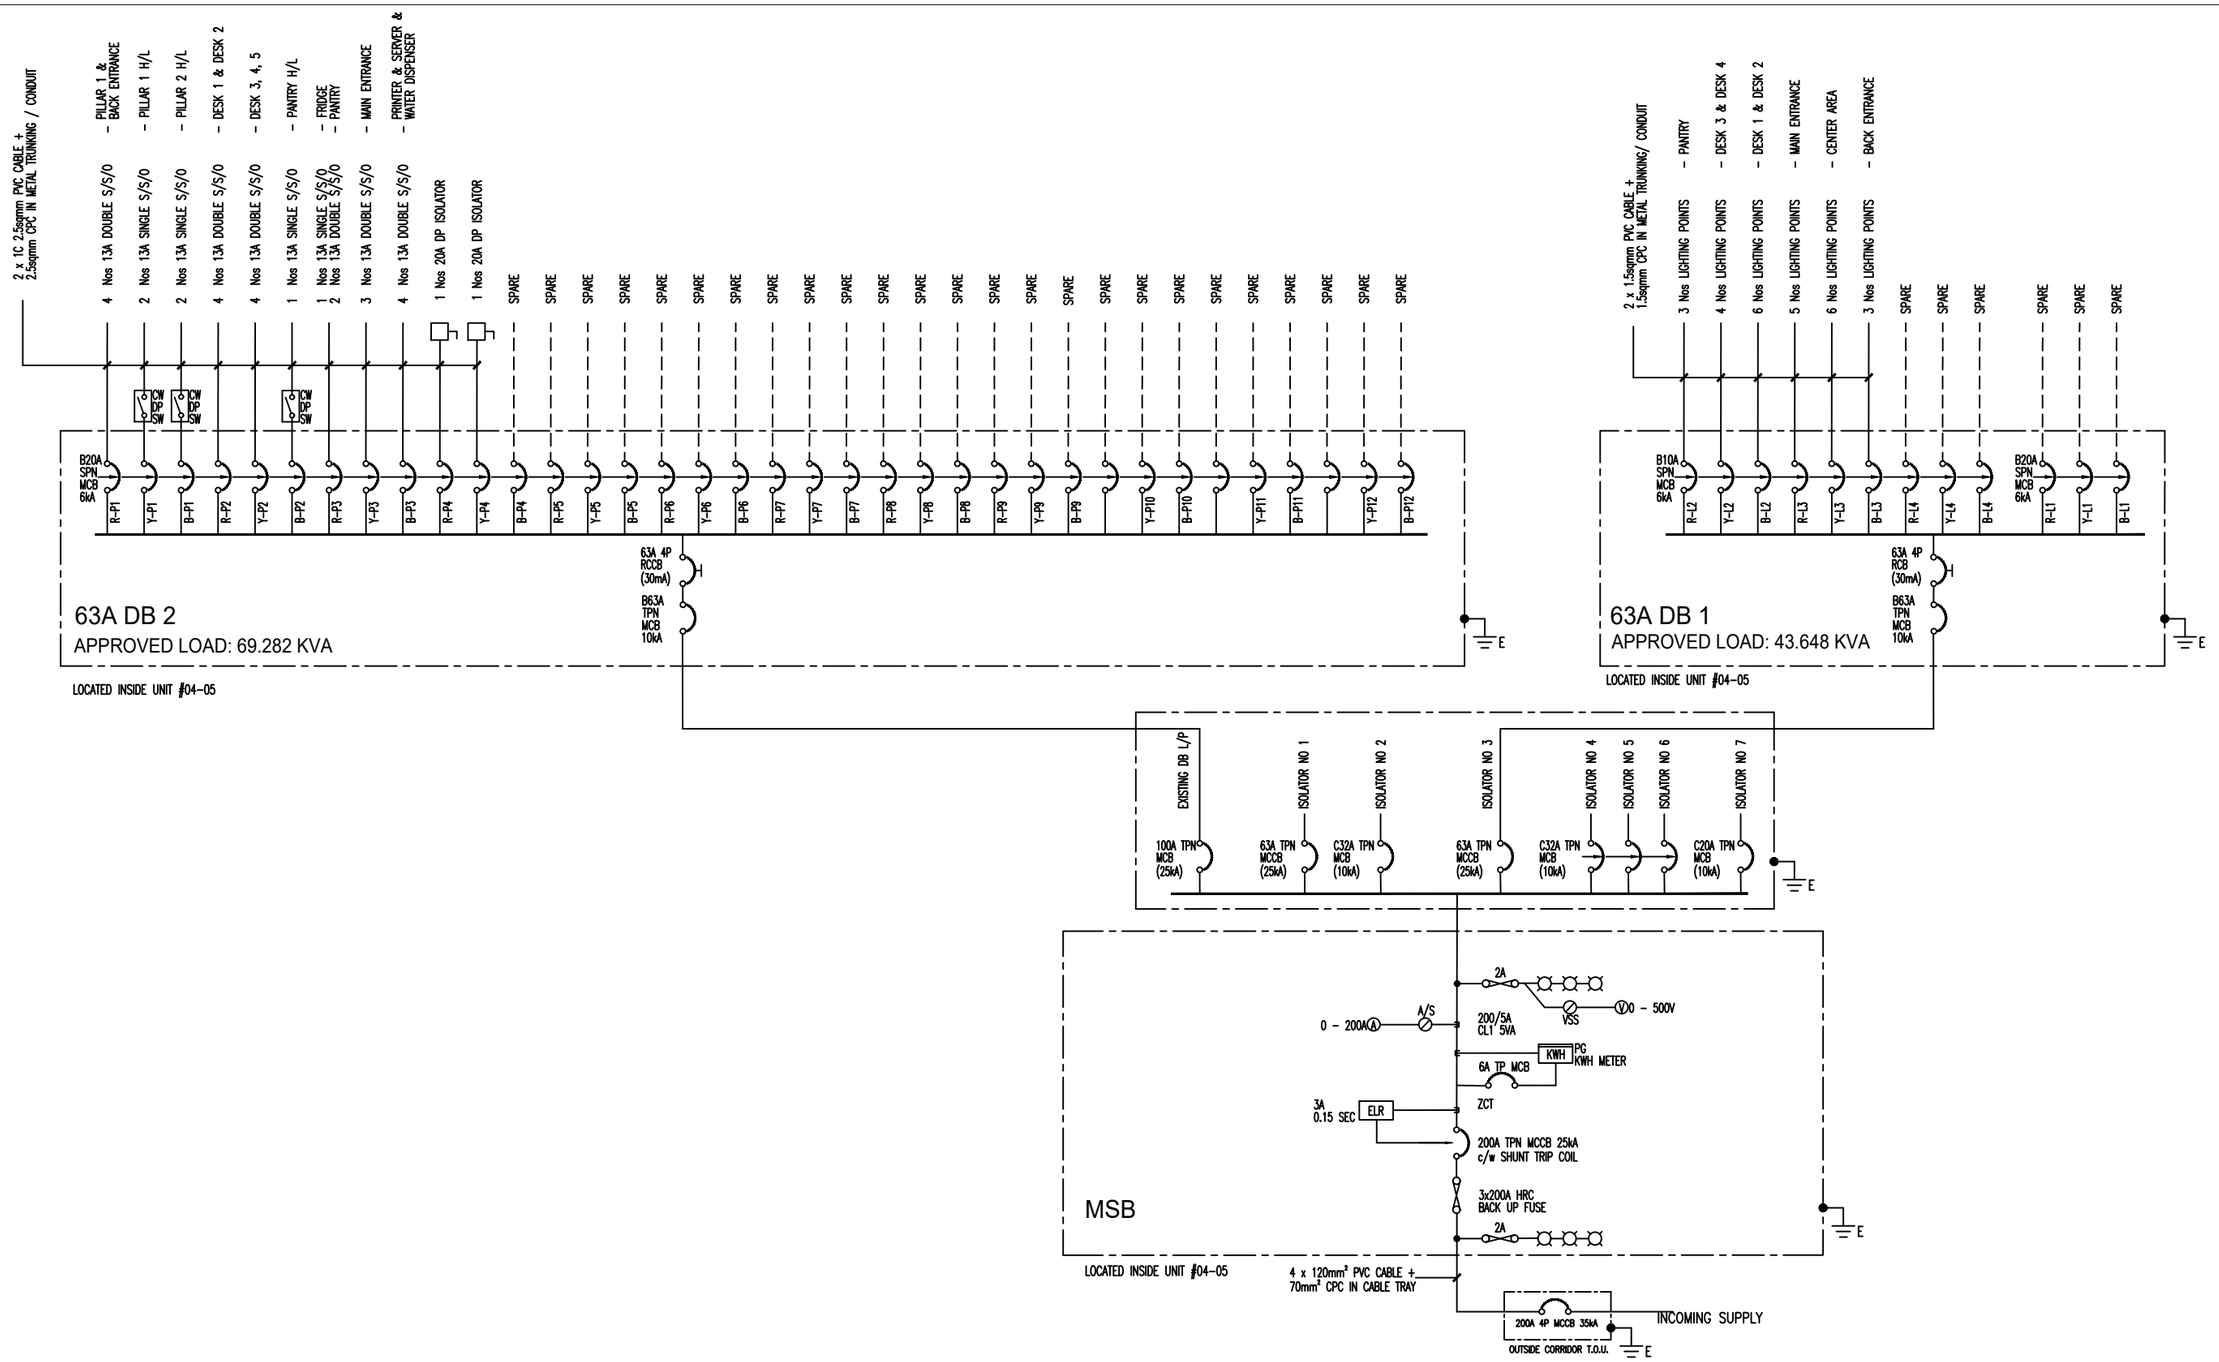

CLIENT :	PROJECT TITLE :				DATE :
VALENTI PTE LTD	ELECTRICAL INSTALLATION AT 449 TAGORE INDUSTRIAL AVENUE #04-05 GREATLAND INDUSTRIAL BUILDING SINGAPORE 787820				8 DEC 2025
				DRAWING NO. : VAL-TAG-MSB-DB	REV : 0