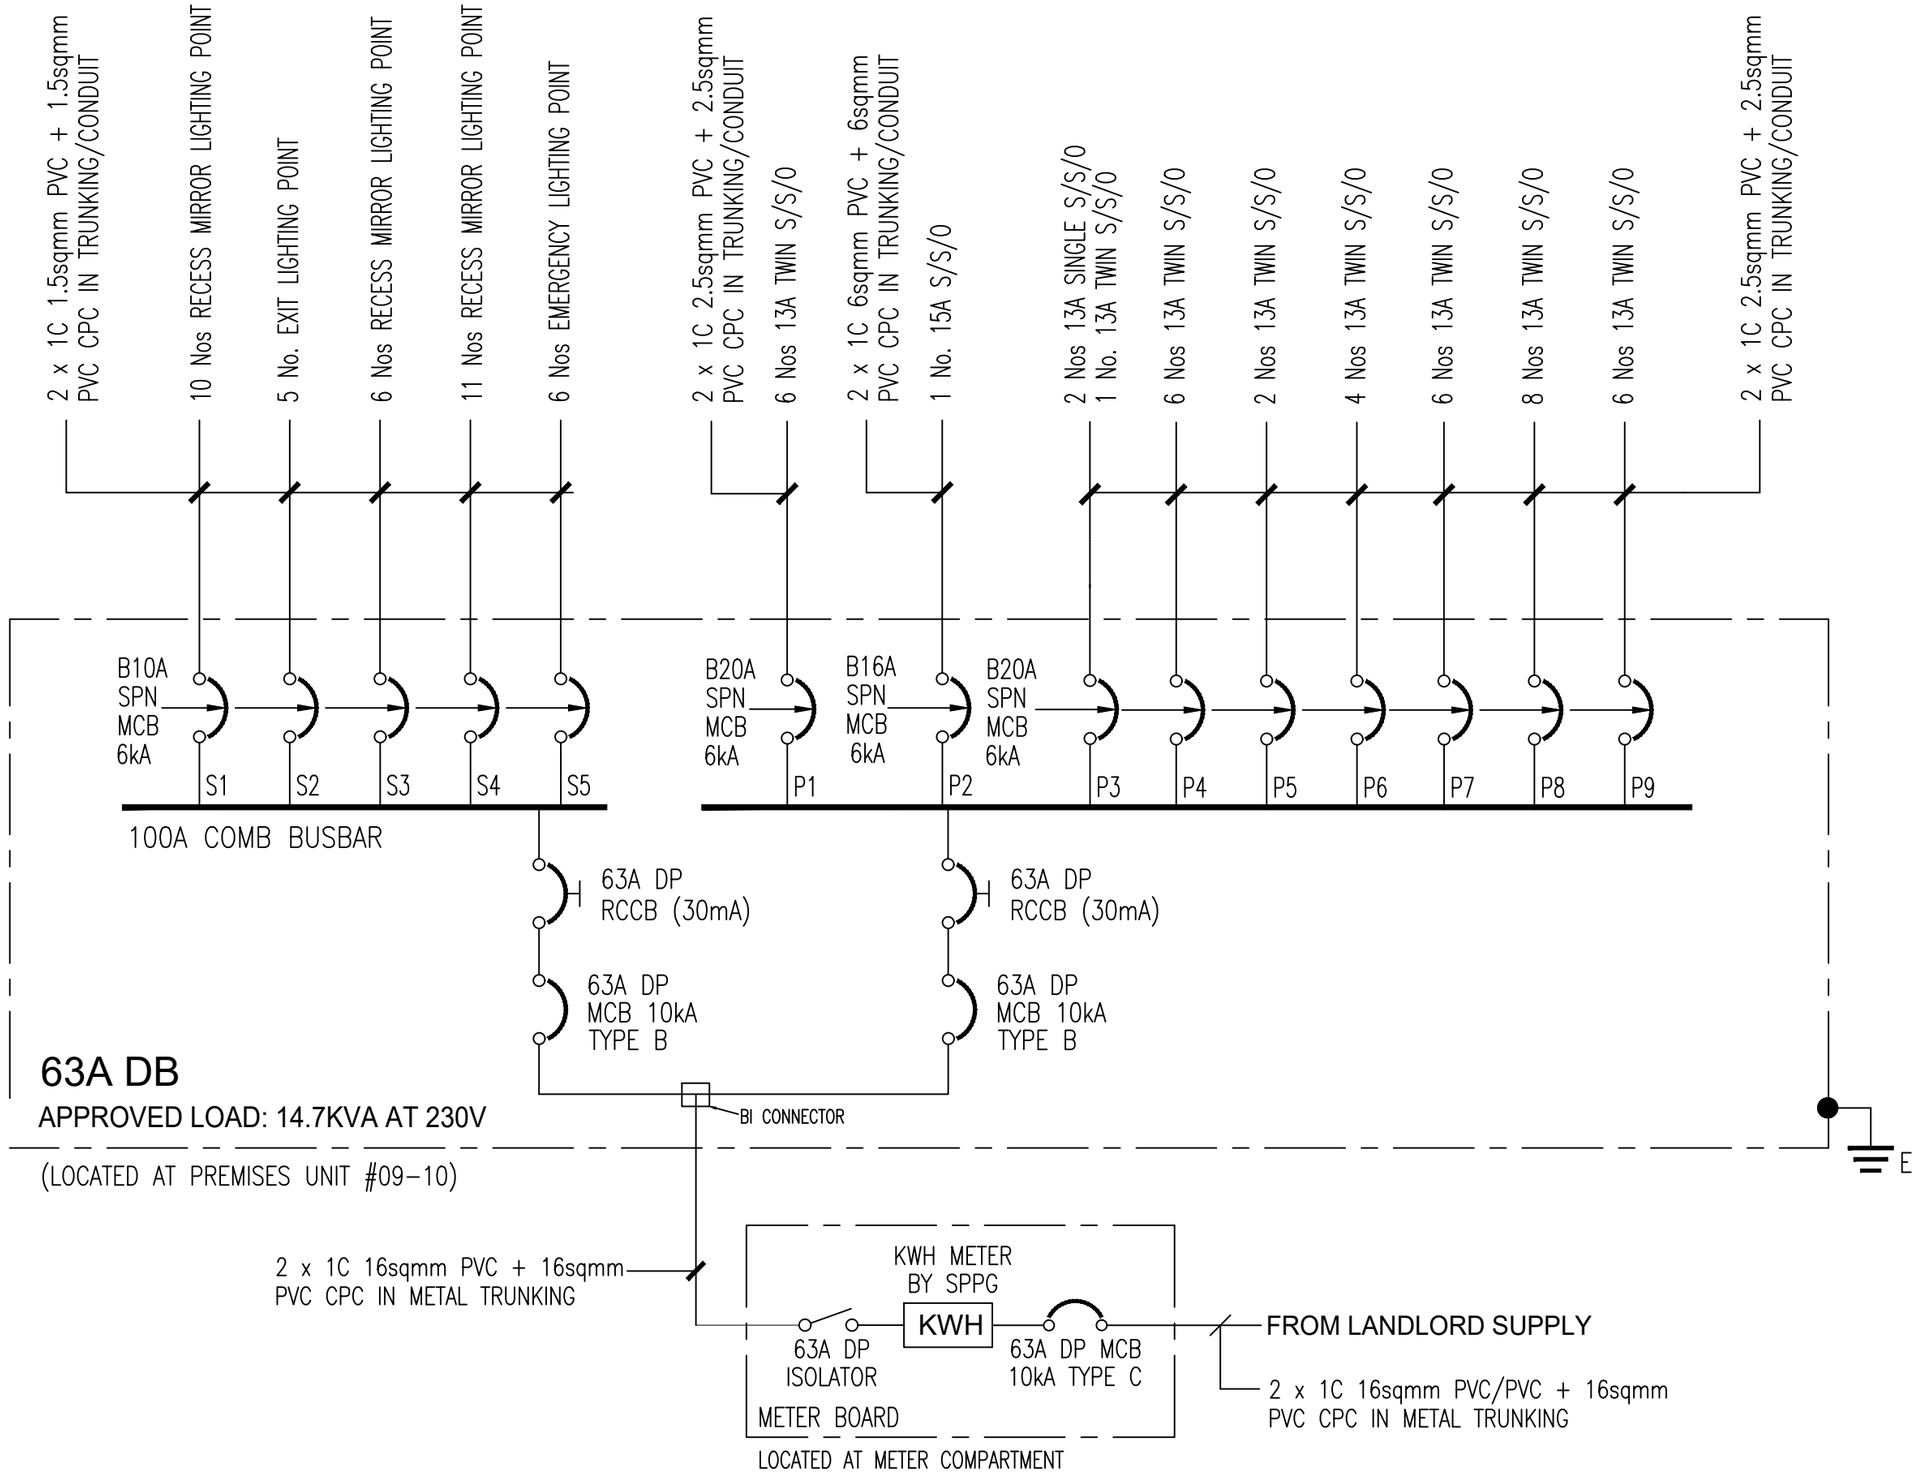

CLIENT / ADDRESS :	CONSULTANT :	ELECTRICAL CONTRACTOR :	DRAWING TITLE :		CHECKED :	DATE :
Crossborders LLC No. 133 New Bridge Road #09-10 Chinatown Point Singapore 059413	Long Home Construction Wares Pte Ltd	I2R M&E PTE. LTD. 709 Yishun Avenue 5 #01-K1 Singapore 760709	ELECTRICAL SERVICES 63A DB SINGLE LINE DIAGRAM		Ryan	25 Oct 2024
					DRAWING NO. : i2R-E-SLD1	REV : 0