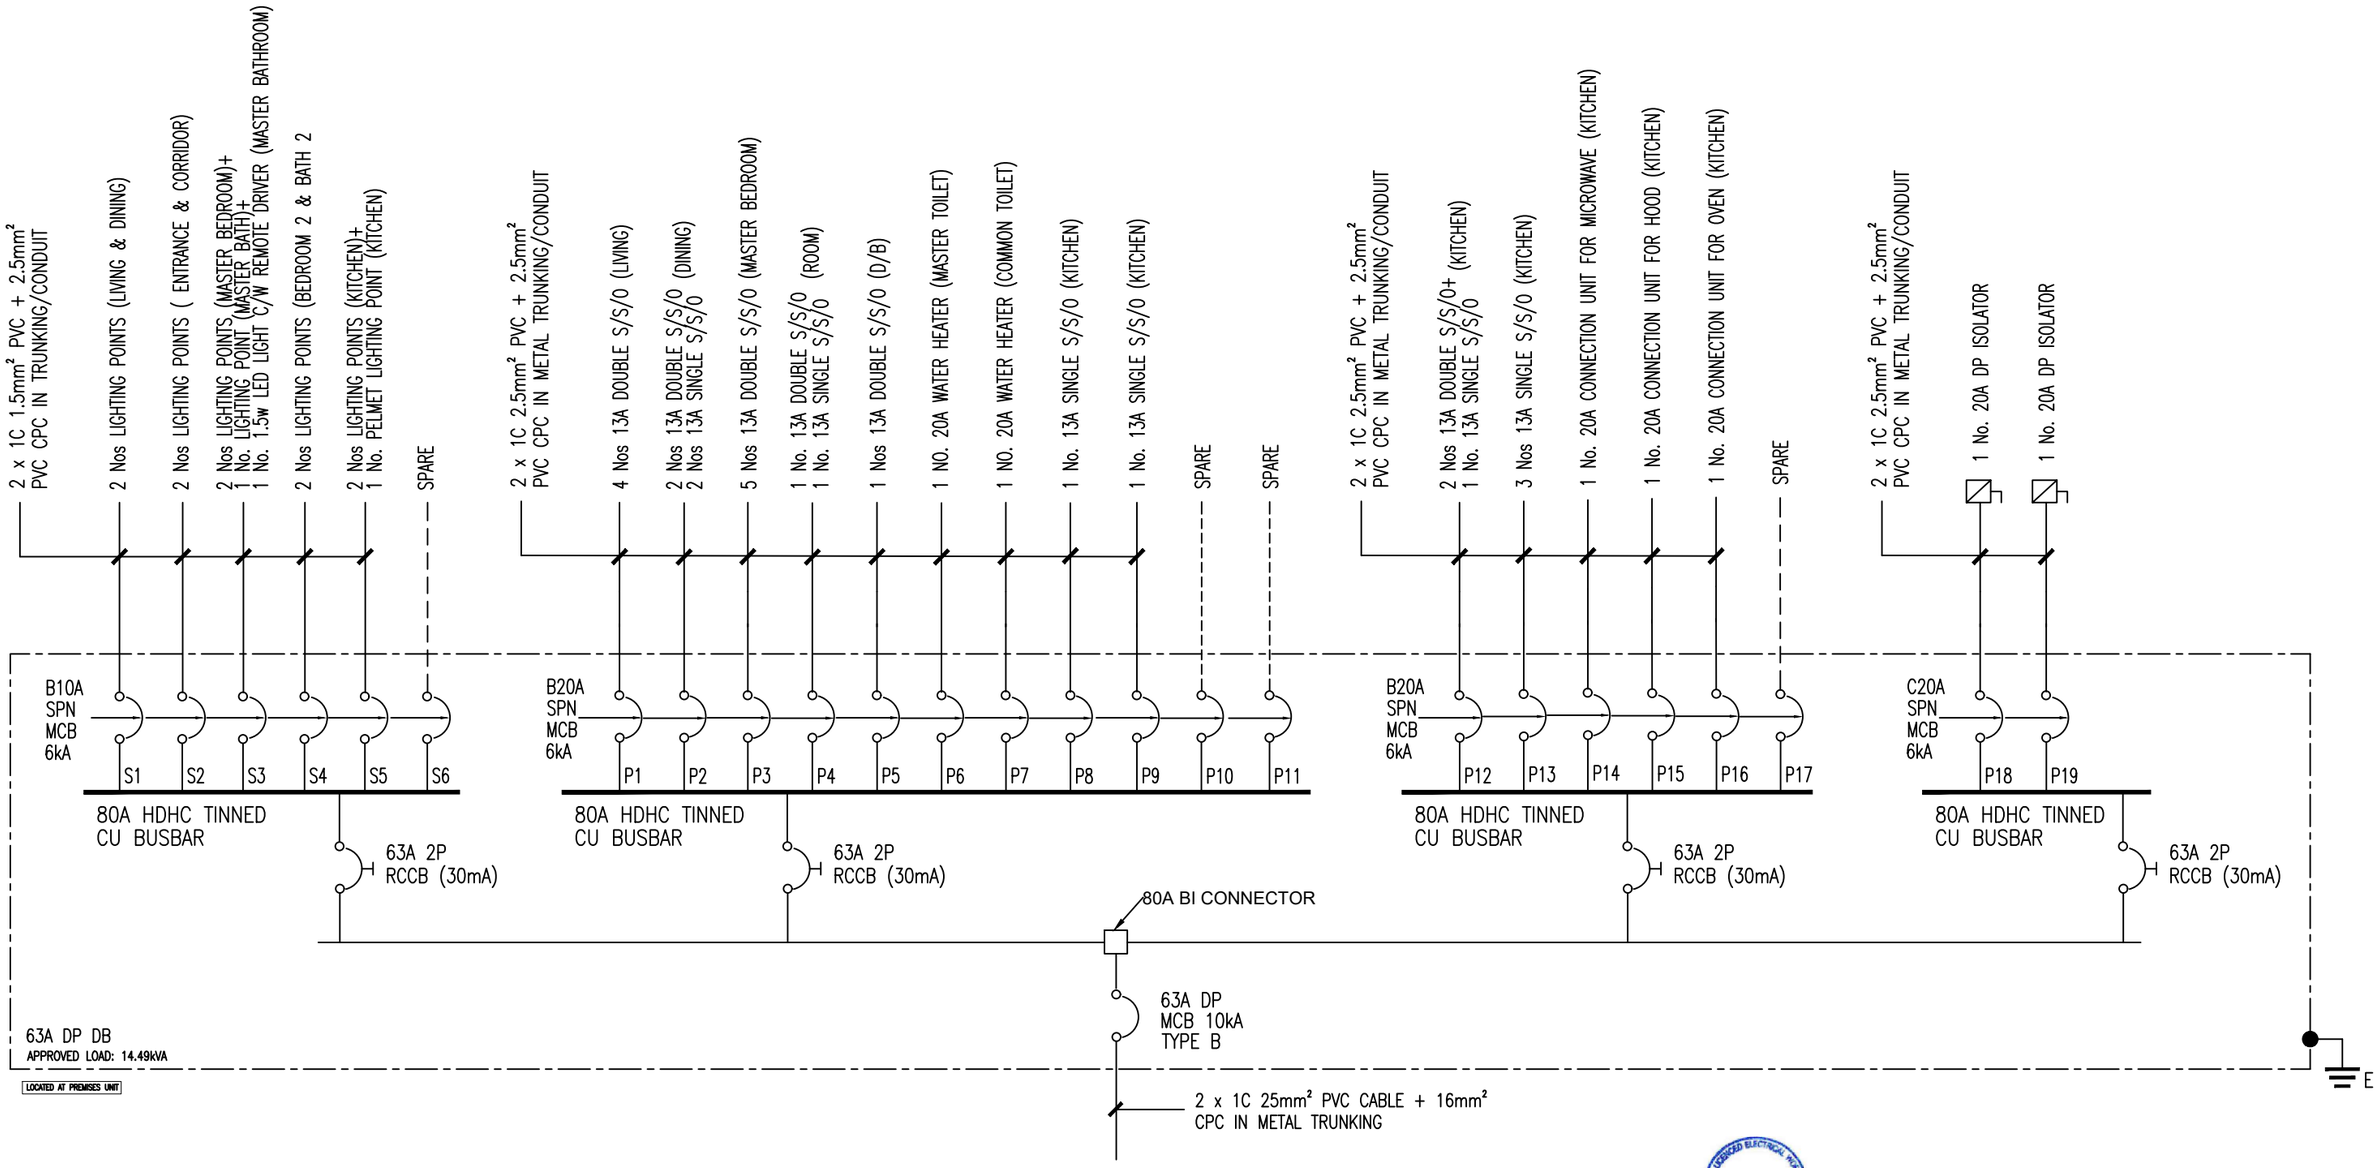

CLIENT / ADDRESS :			DRAWING TITLE :	LEW :	DRAWED BY:	DATE :
13 LEEDON HEIGHT #22-44 SINGAPORE 266224			SINGLE LINE DIAGRAM (SLD)	NAME : SEOW SWEE LEONG LEW NO : 8/25825	cs	23 FEB 2026
					DRAWING NO. : I2R-DLD-2244-SLD	REV : 0