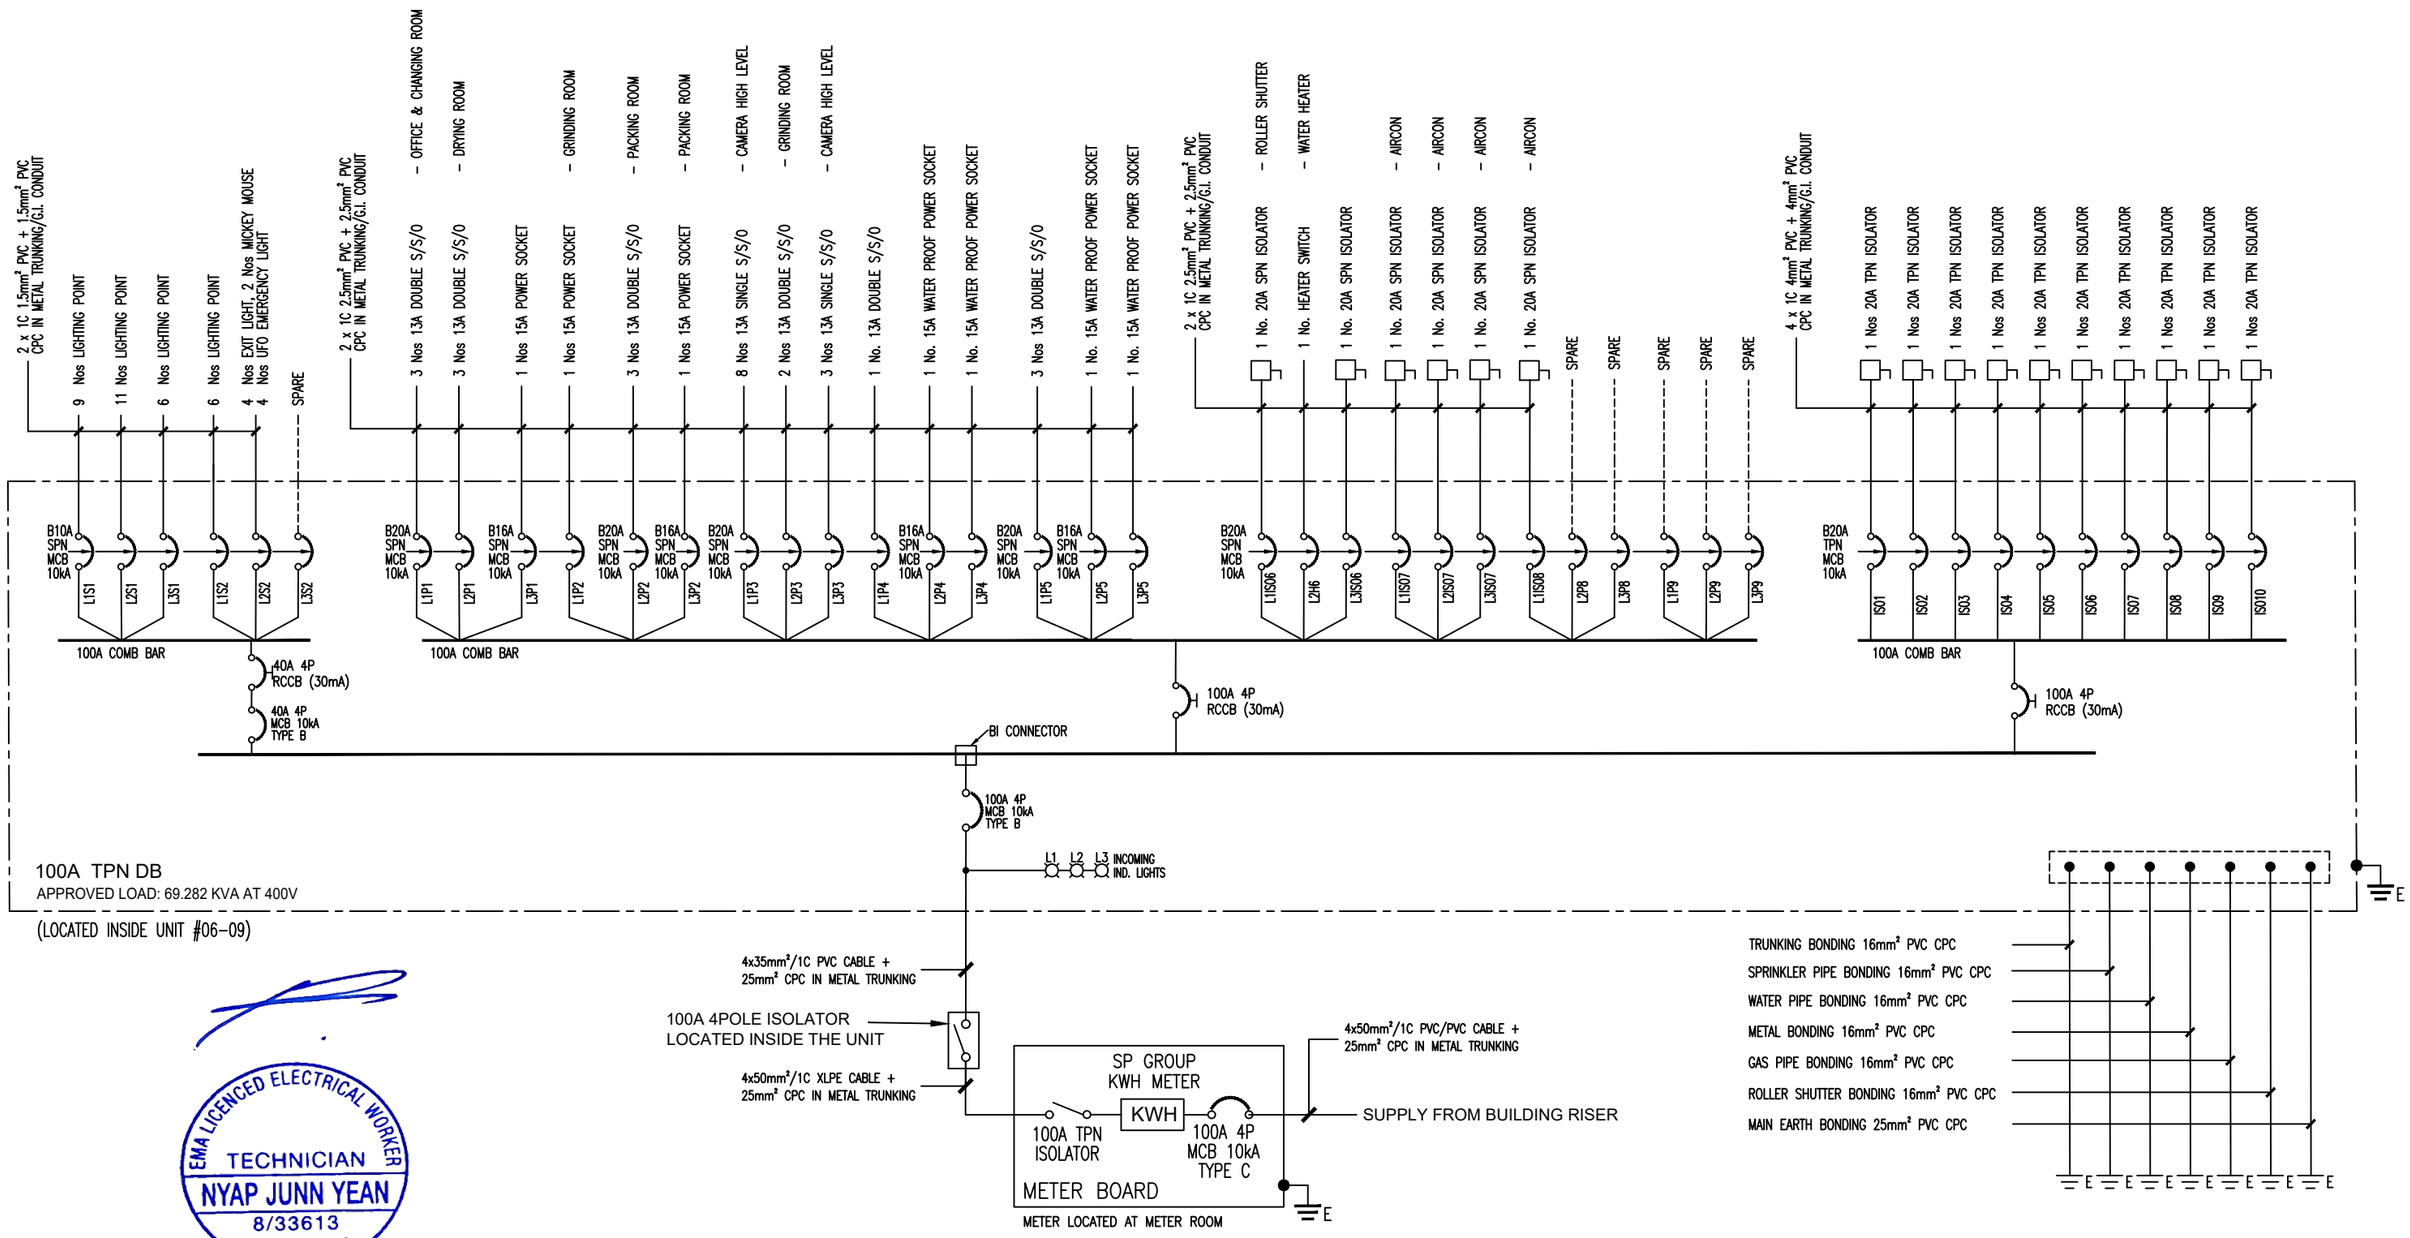

EMA LICENCED ELECTRICAL WORKER
TECHNICIAN
NYAP JUNN YEAN
8/33613
SINGAPORE

CLIENT / ADDRESS :	MAIN CONTRACTOR :	ELECTRICAL CONTRACTOR :	DRAWING TITLE :	LEW :	CHECKED :	DATE :
HOON FOOD INDUSTRIES PTE LTD 21 Mandai Estate #06-09 Food Vision @ Mandai Singapore 729913	I2R M&E PTE. LTD. 709 Yishun Avenue 5 #01-K1 Singapore 760709 TEL: 9777 1983	I2R M&E PTE. LTD. 709 Yishun Avenue 5 #01-K1 Singapore 760709 TEL: 9777 1983	PERMANENT DB SLD	NYAP JUNN YEAN EMA Licence No. : 8/33613	Ryan	9 FEB 2025
					DRAWING NO. : I2R-HFI-MAN-SLD	REV : 0