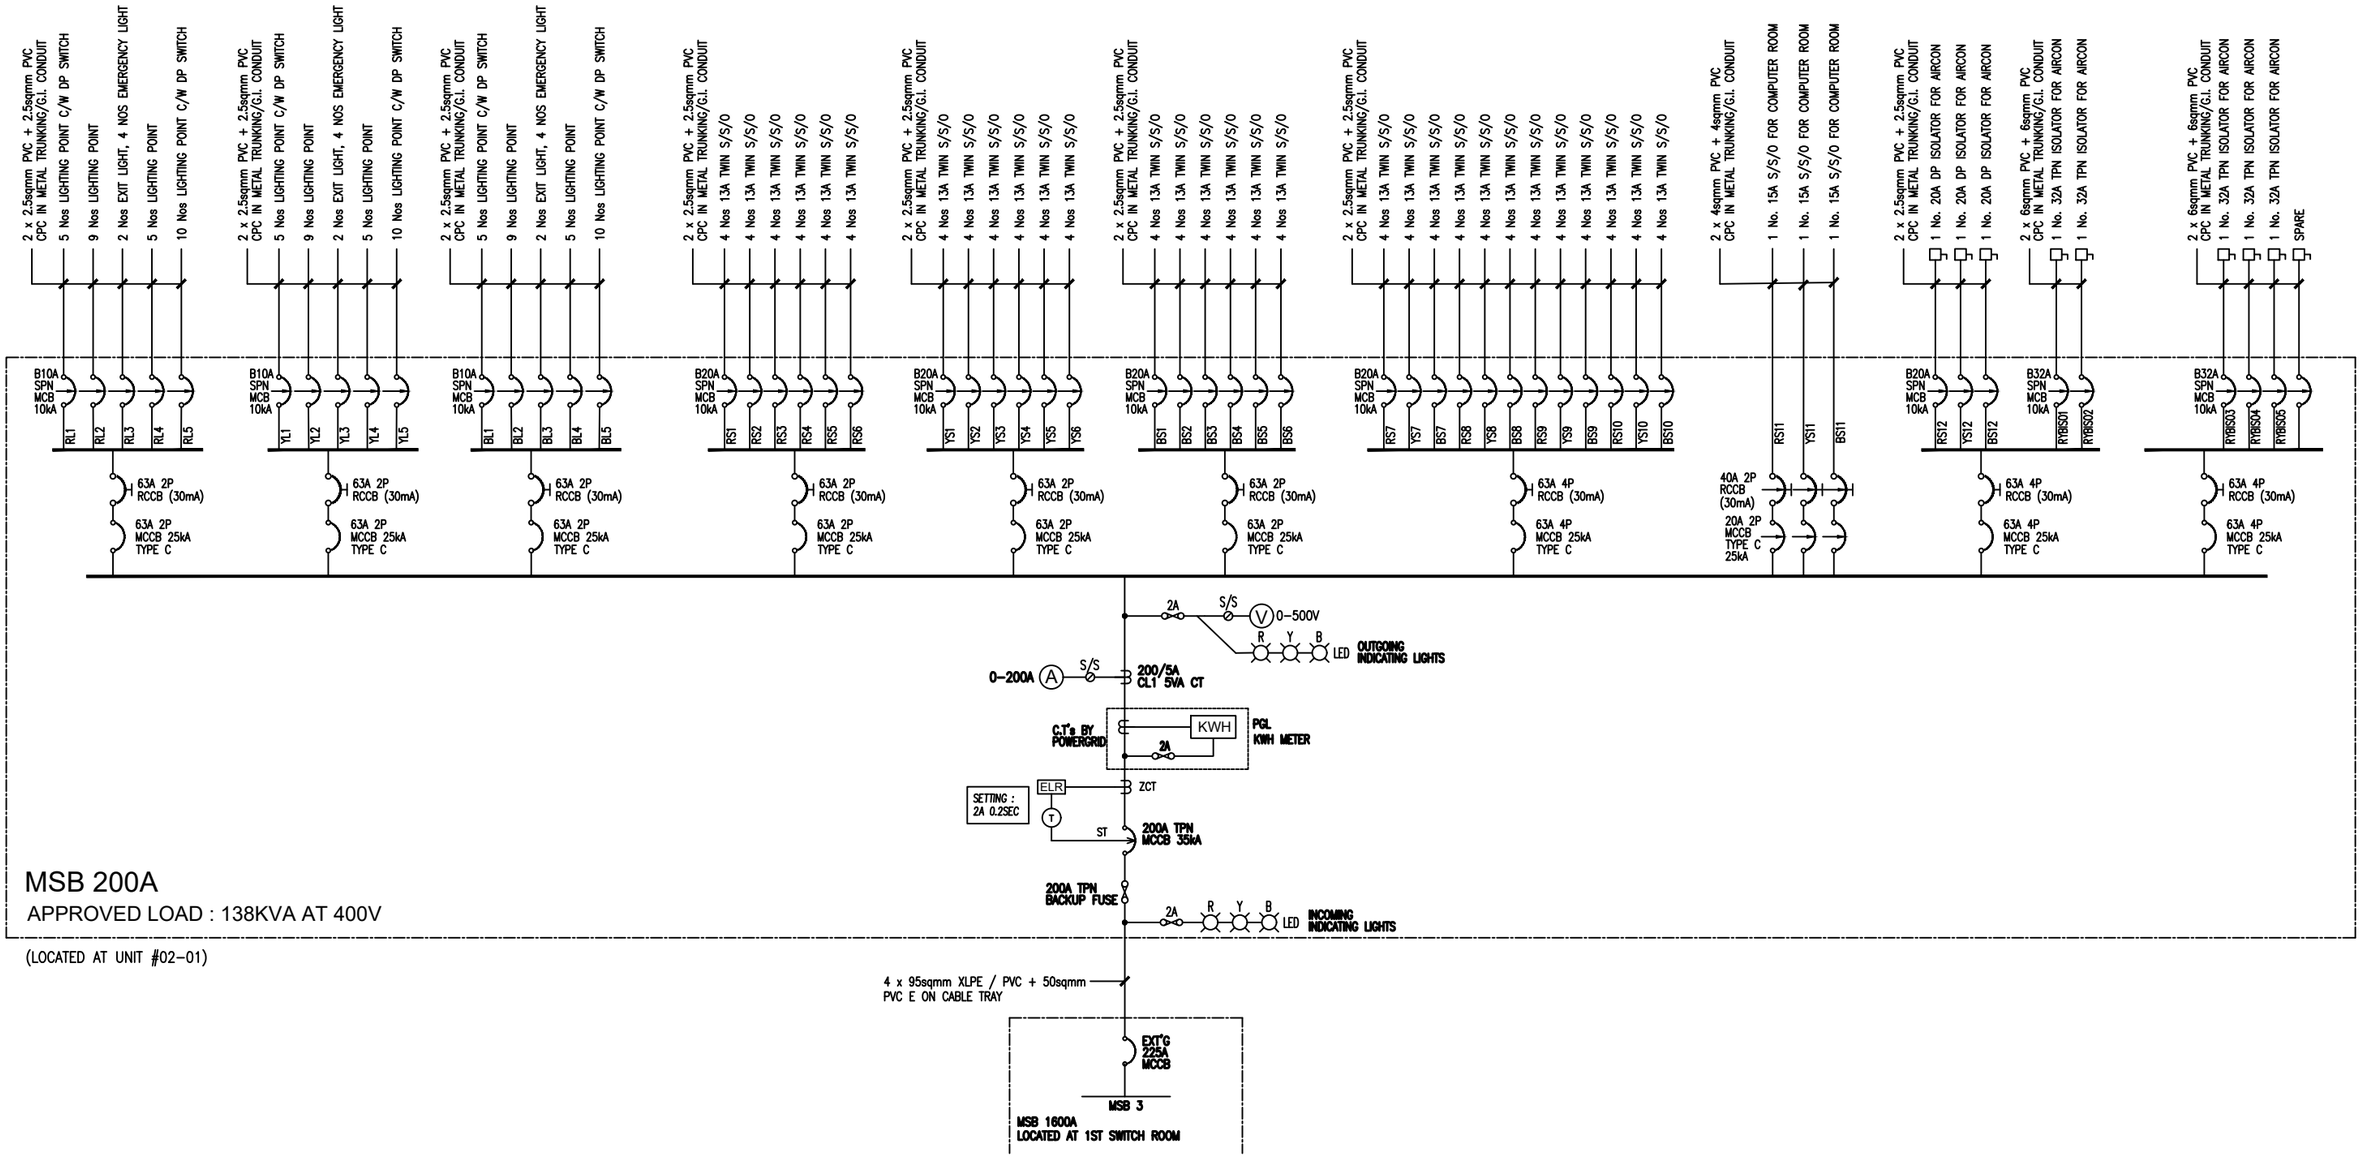

CLIENT / ADDRESS :	MAIN CONTRACTOR :	ELECTRICAL CONTRACTOR :	DRAWING TITLE :	LEW :	CHECKED :	DATE :
INOVA COLLECTIVE PTE LTD 8 Jalan Kilang Timor #02-10, Kewalram House, Singapore 159305		I2R M&E PTE. LTD. 709 Yishun Avenue 5 #01-K1 Singapore 760709 TEL: 9777 1983	SINGLE LINE DIAGRAM (SLD)	SEOW SWEE LEONG EMA Licence No. : 8/25825	Ryan	29 JULY 2025
					DRAWING NO. : I2R-INVC-JKT-SLD	REV : 0