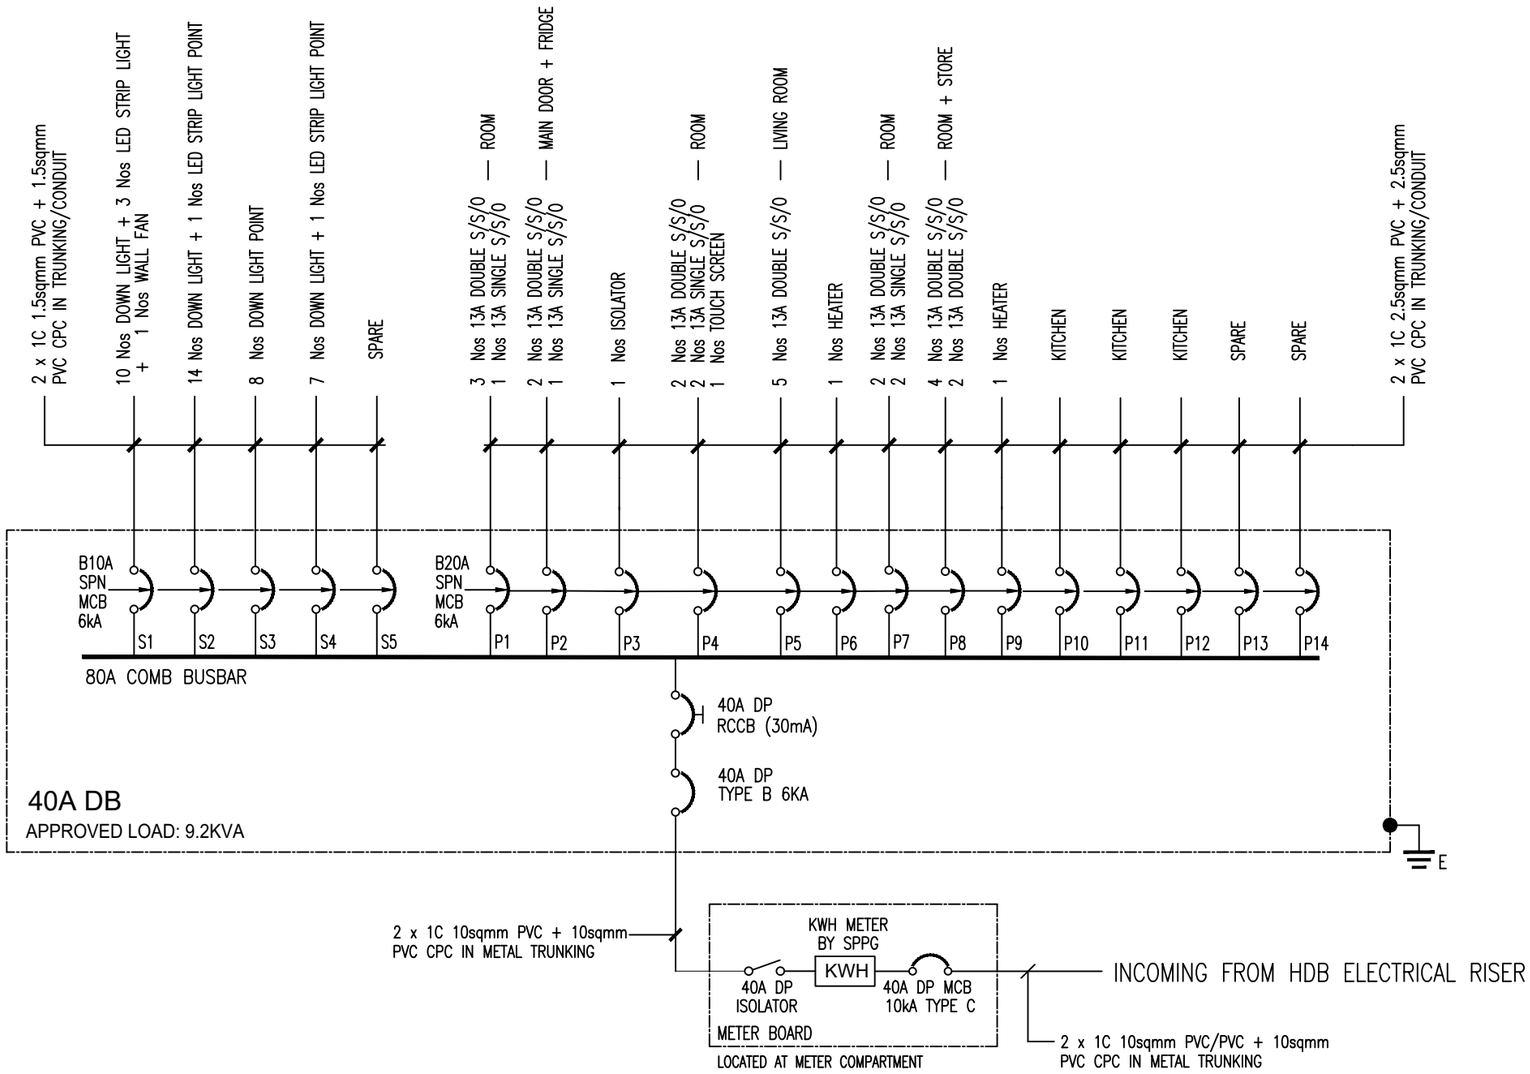

CLIENT / ADDRESS :	CONSULTANT :	ELECTRICAL CONTRACTOR :	DRAWING TITLE :	LEW :	CHECKED :	DATE :
162 YUNG PING RD #12-21 SINGAPORE 610162		I2R M&E PTE. LTD. 709 Yishun Avenue 5 #01-K1 Singapore 760709	40A DP Single Line Diagrams		Ryan	28 DEC 2024
					DRAWING NO. : i2R-CSM-SLD01	REV : 0