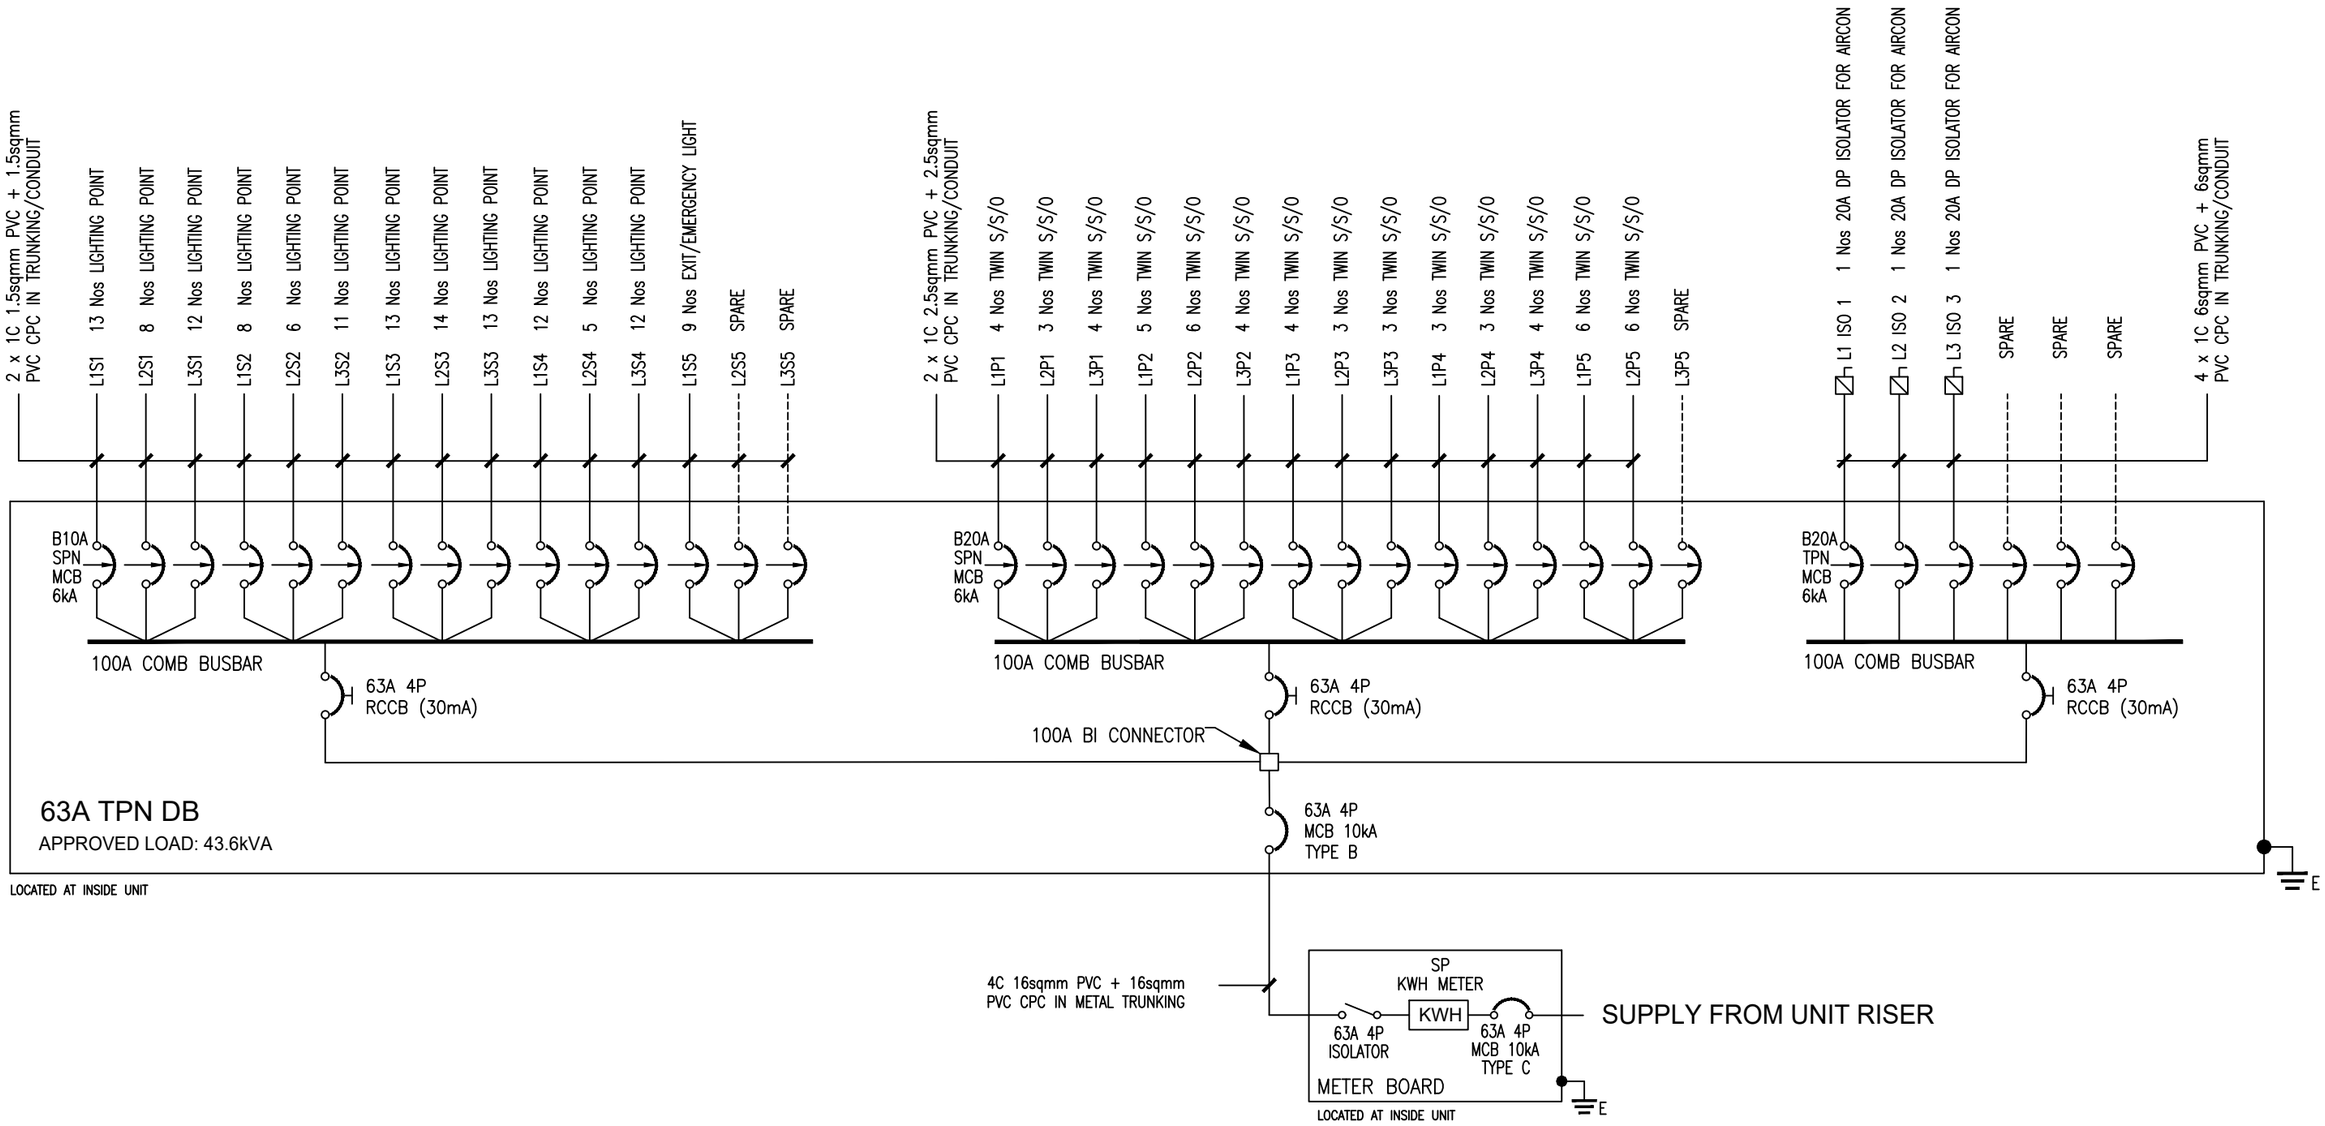

CLIENT / ADDRESS :	MAIN CONTRACTOR :	ELECTRICAL CONTRACTOR :	DRAWING TITLE :	LEW :	CHECKED :	DATE :
EASTPOINT MALL #B1-19/20/21 3 SIMEI ST 6 S 528833	LOTTI PTE LTD 4, LORONG 7 TOA PAYOH COURT S 310004	LEPPEK CONSTRUCTION PTE LTD 60 PAYA LEBAR SQUARE #07-43C SINGAPORE 409051	PERMANENT SINGLE LINE DIAGRAM			27 MAY 2025
					DRAWING NO. : I2R-EPM-LOT-SLD	REV : 0