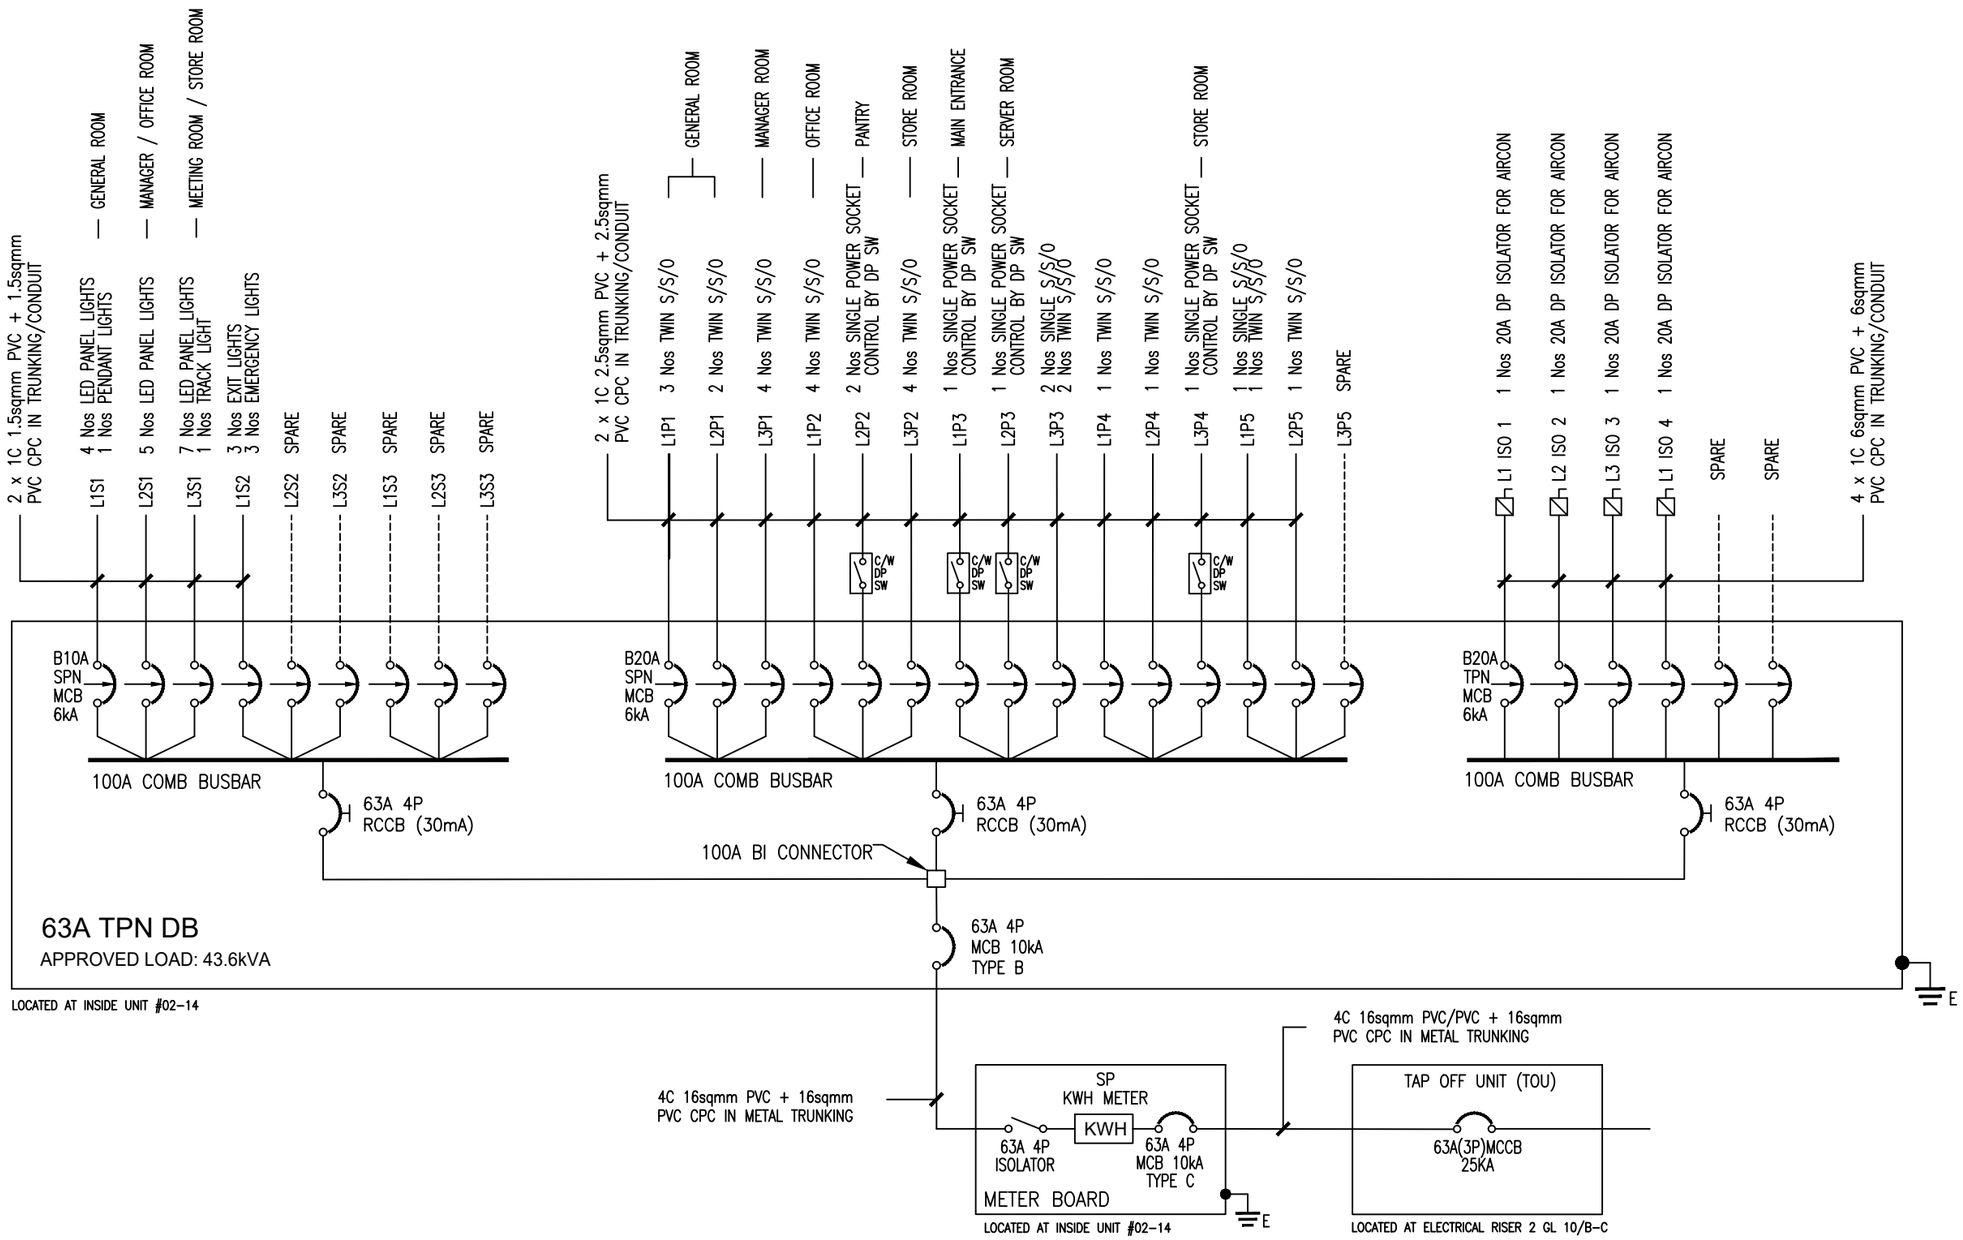

CLIENT / ADDRESS :	CONSULTANT :	ELECTRICAL CONTRACTOR :	DRAWING TITLE :	LEW :	CHECKED :	DATE :
CLEAR RESOLVE PTE LTD The Gemini, 41 Science Park RD #02-14 S 117610		I2R M&E PTE. LTD. 709 Yishun Avenue 5 #01-K1 Singapore 760709 HP: 9777 1983	SINGLE LINE DIAGRAM (SLD)	Ryan, Nyap Junn Yean EMA Licence No. : 8/33613 Mobile Number. : 91597207	Ryan	6 JAN 2025
					DRAWING NO. : i2R-CS-CPR-SLD-01	REV : 0