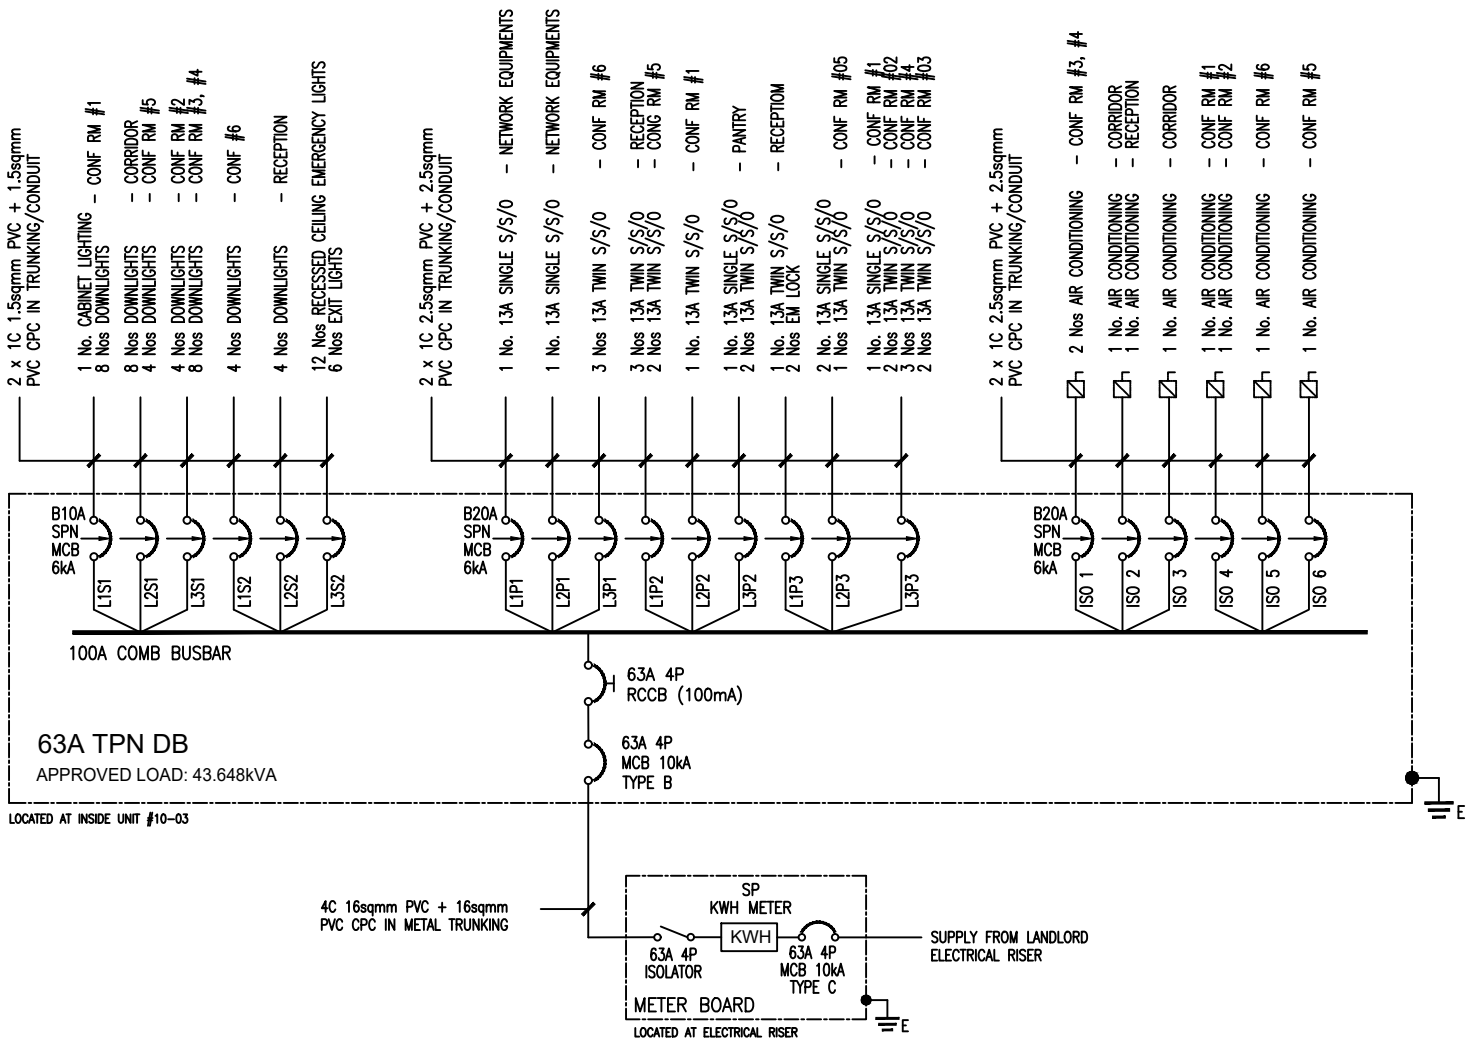

CLIENT / ADDRESS :	MAIN CONTRACTOR :	ELECTRICAL CONTRACTOR :	DRAWING TITLE :	LEW :	CHECKED :	DATE :
SUNLOVE ABODE FOR INTELLECTUALLY INFIRMED LTD 140 PAYA LEBAR ROAD #10-03 SINGAPORE 409015	NAKANO SINGAPORE PTE LTD 1 COLEMAN STREET #06-02 THE ADELPHI SINGAPORE 179803	OPTO GLOBAL TECH PTE LTD 15 YISHUN INDUSTRIAL STREET 1 #03-10 WIN5 SINGAPORE 249580	SINGLE LINE DIAGRAM (SLD)	SEOW SWEE LEONG EMA LICENSE NO: 8/25825	Ryan	9 OCT 2025
					DRAWING NO. : OGT-SH1003-SLD	REV : 0