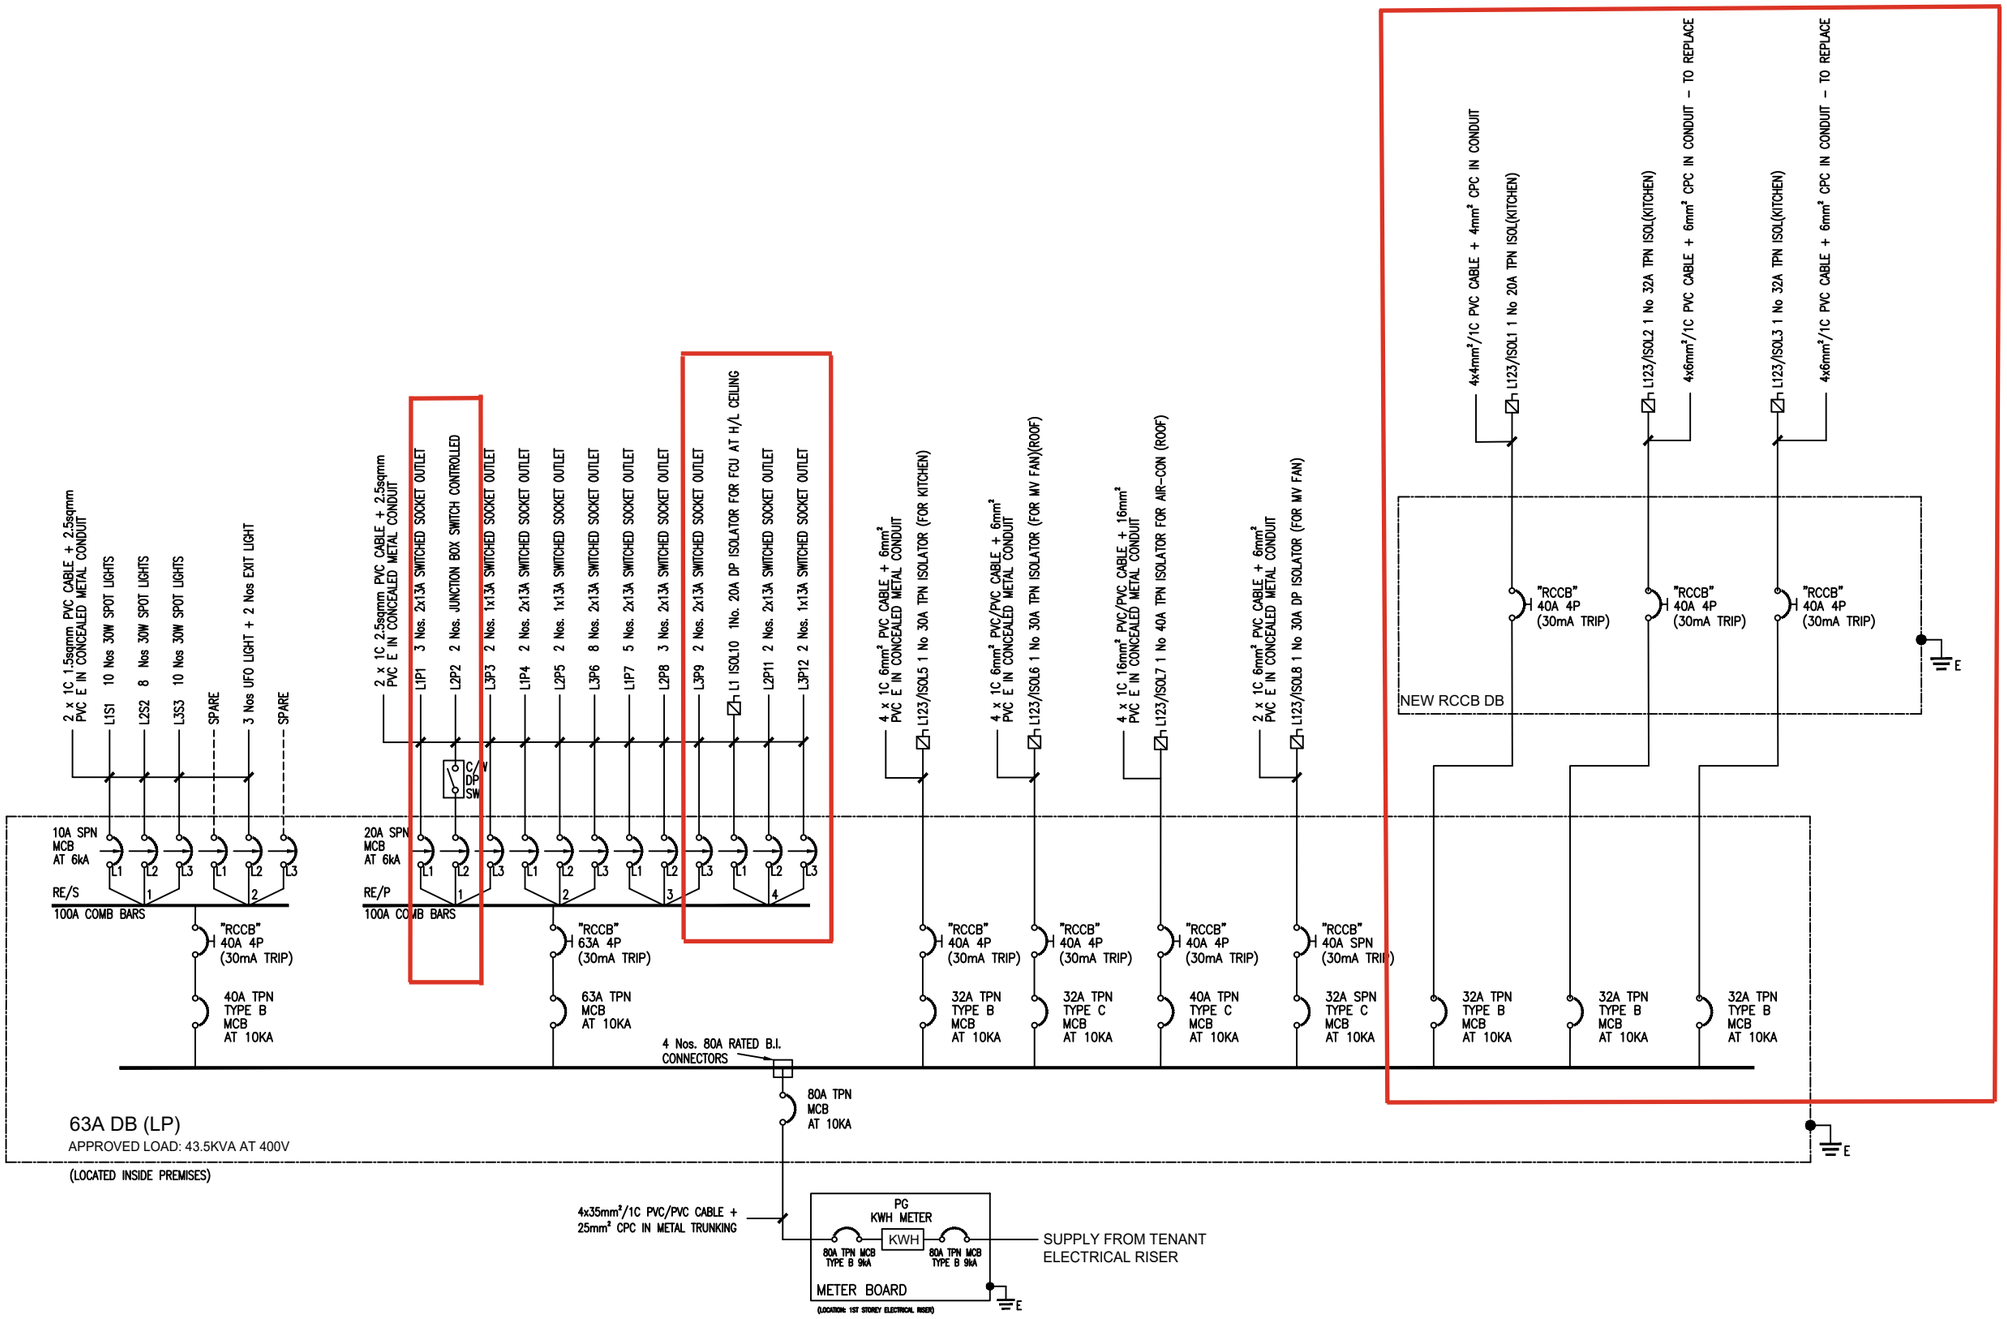

CLIENT / ADDRESS :	MAIN CONTRACTOR :	ELECTRICAL CONTRACTOR :	DRAWING TITLE :	LEW :	CHECKED :	DATE :
PROJECT 68 SBR PTE. LTD. 68 South Bridge Road #01-01 (S) 058698			SINGLE LINE DIAGRAM (SLD)			6/4/2025
					DRAWING NO. :	REV : 0