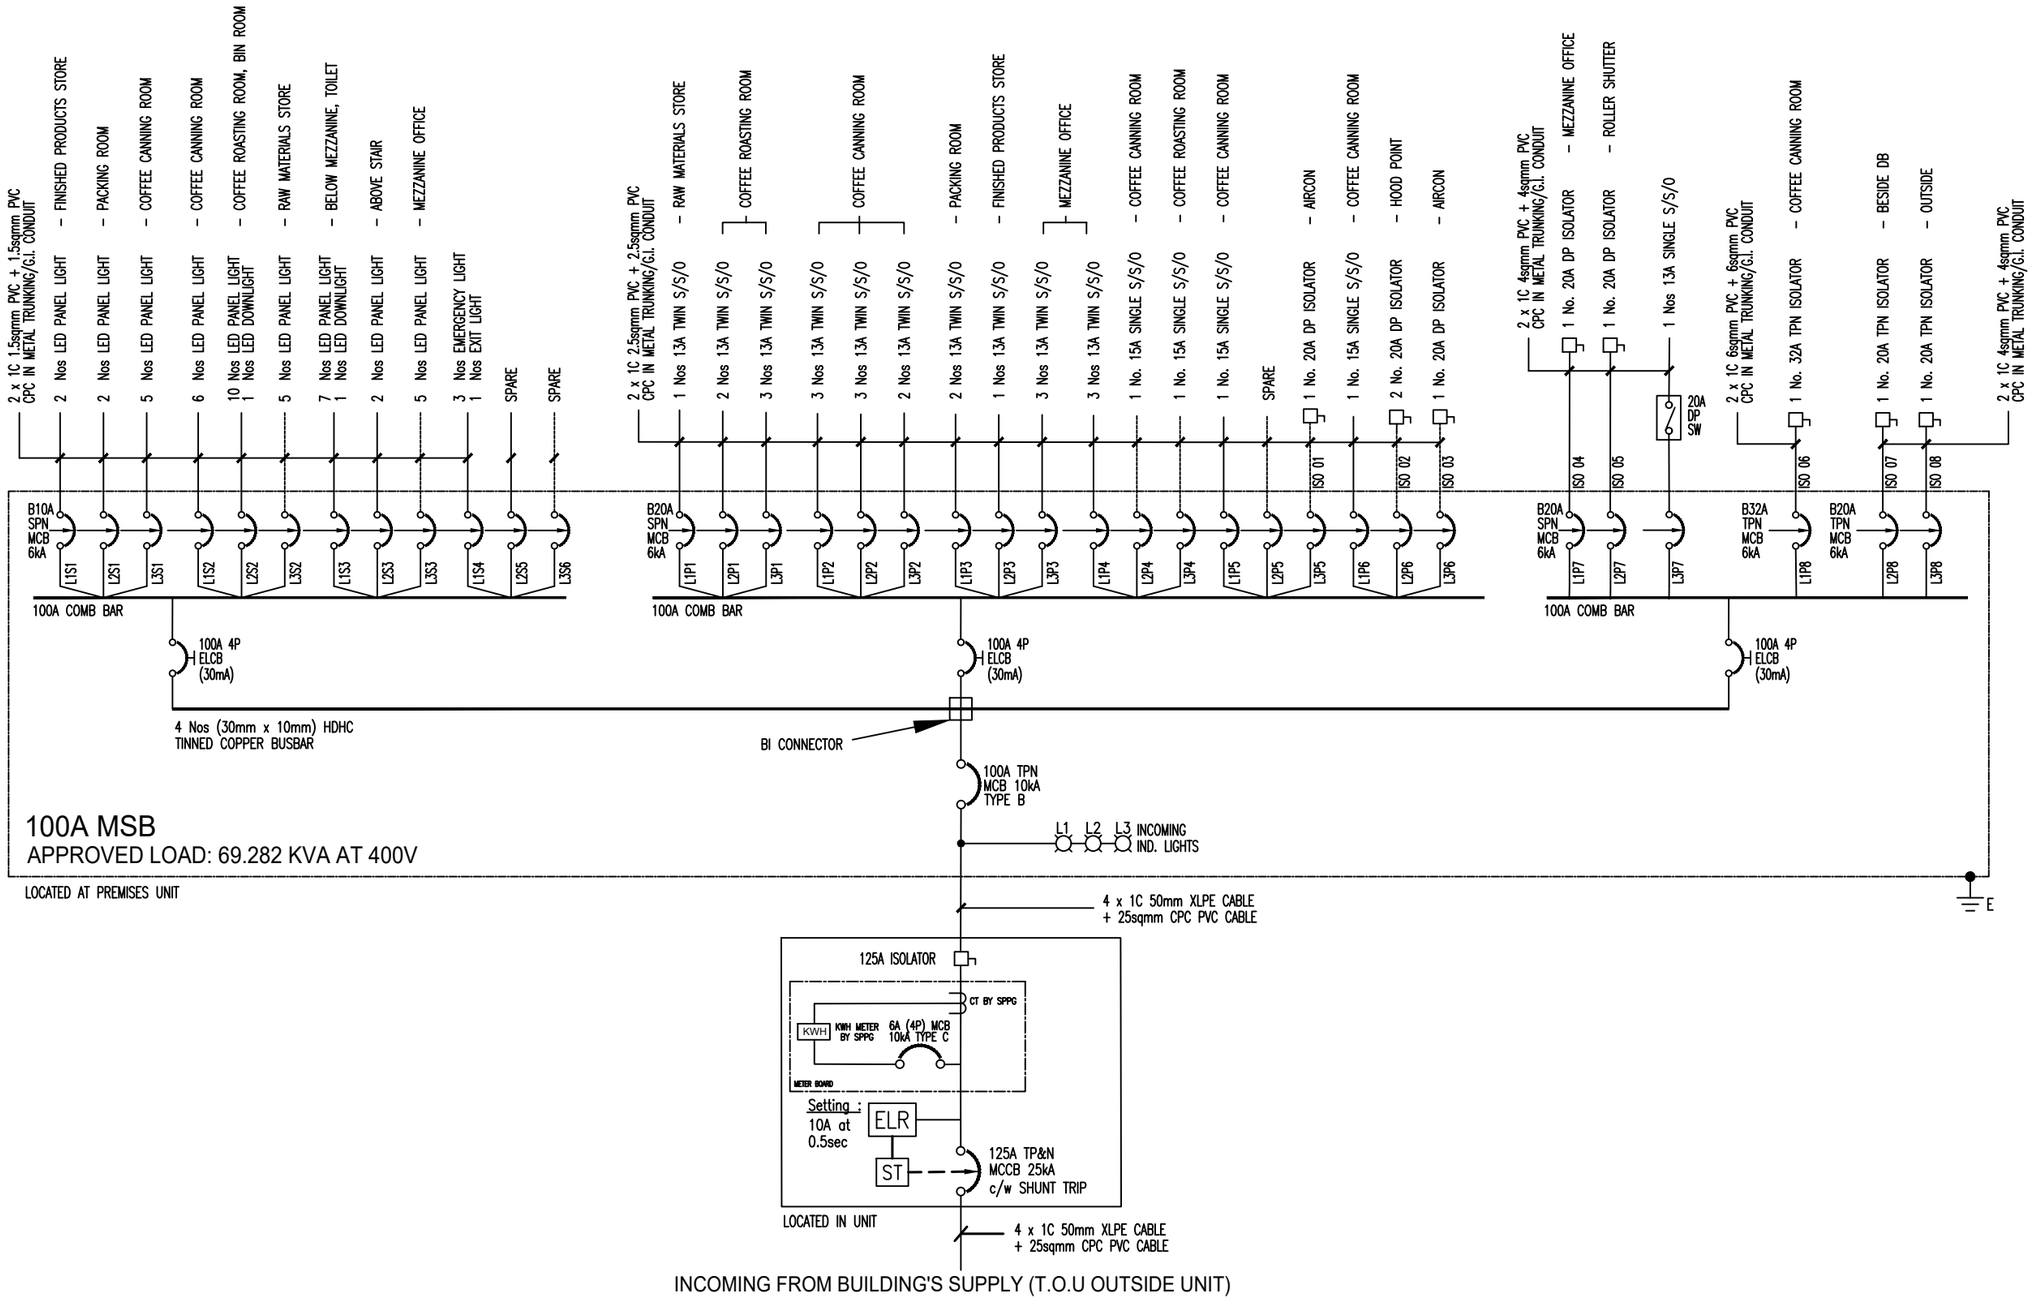

CLIENT / ADDRESS :	MAIN CONTRACTOR :	ELECTRICAL CONTRACTOR :	DRAWING TITLE :	LEW :	CHECKED :	DATE :
NECESSARY PROVISIONS PTE. LTD. 200 PANDAN LOOP #03-01 S1288388	UY CONTRACTOR 210 Geylang Road Singapore 389270	I2R M&E PTE. LTD. 709 Yishun Avenue 5 #01-K1 Singapore 760709 TEL: 9777 1983	SINGLE LINE DIAGRAM (SLD)	Ryan, Nyap Junn Yean EMA Licence No. : 8/33613 Mobile Number. : 91597207	Ryan	23 JAN 2025
					DRAWING NO. : I2R-NPRO-SLD	REV : 0